

18 House / Khuon Studio + Phan Khac Tung

Architects: Khuon Studio, Phan Khac Tung

Location: Ho Chi Minh City, Vietnam

Design Team: Huynh Anh Tuan, Phan Khac Tung, Nguyen

Do Hoang Nam, Nguyen Xuan Truong

Type: Residential, private


Area: 18.0 m²




Year: 2017

Status: Built

Photographs: Hiroyuki Oki, Thiet Vu

Manufacturers: Lixil | INAX, Caesar, Malloca

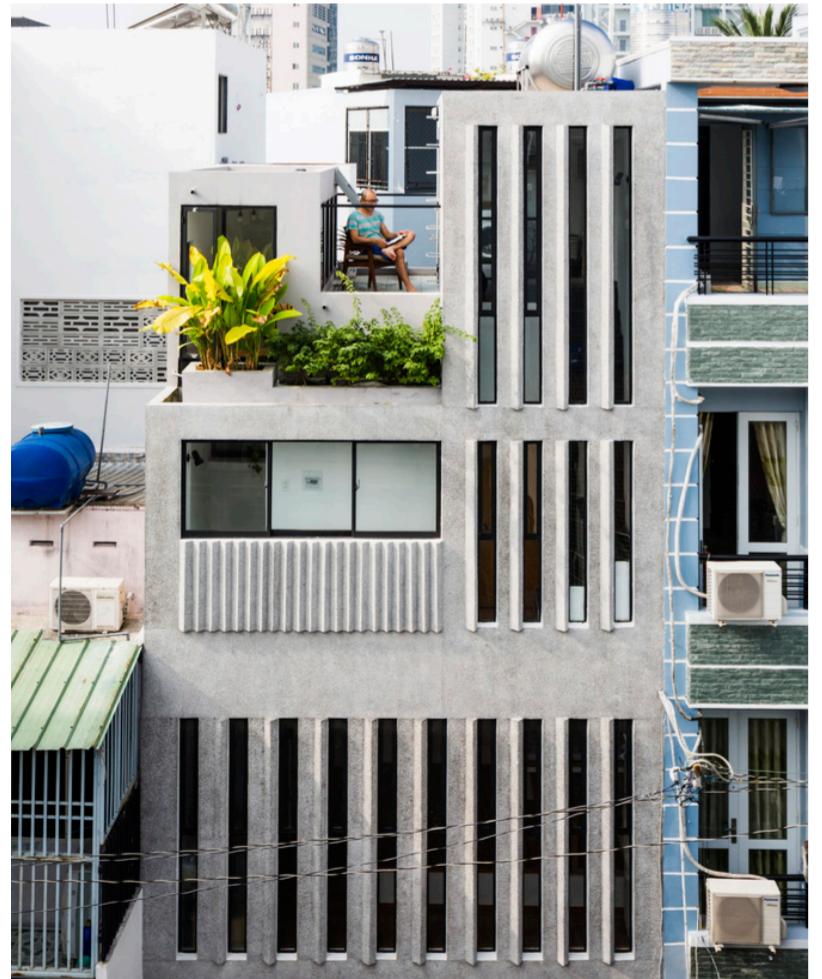

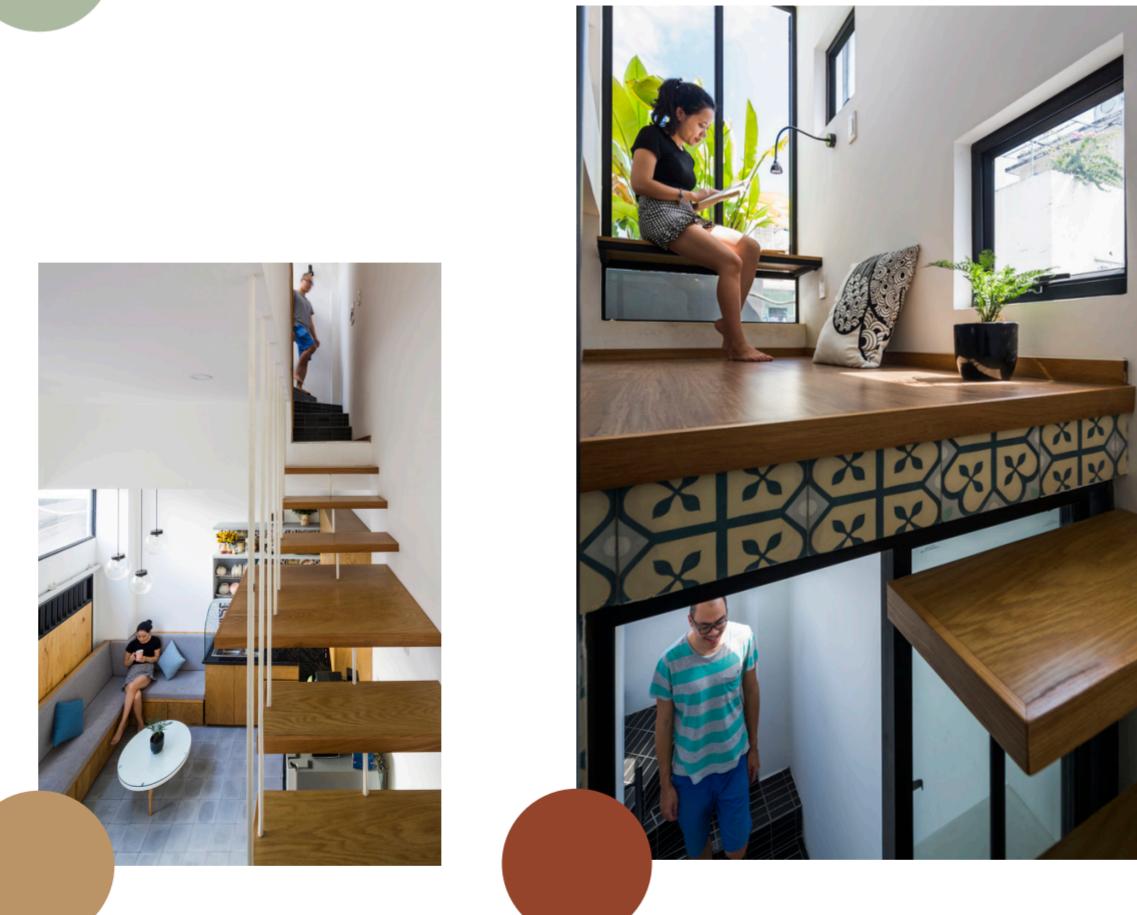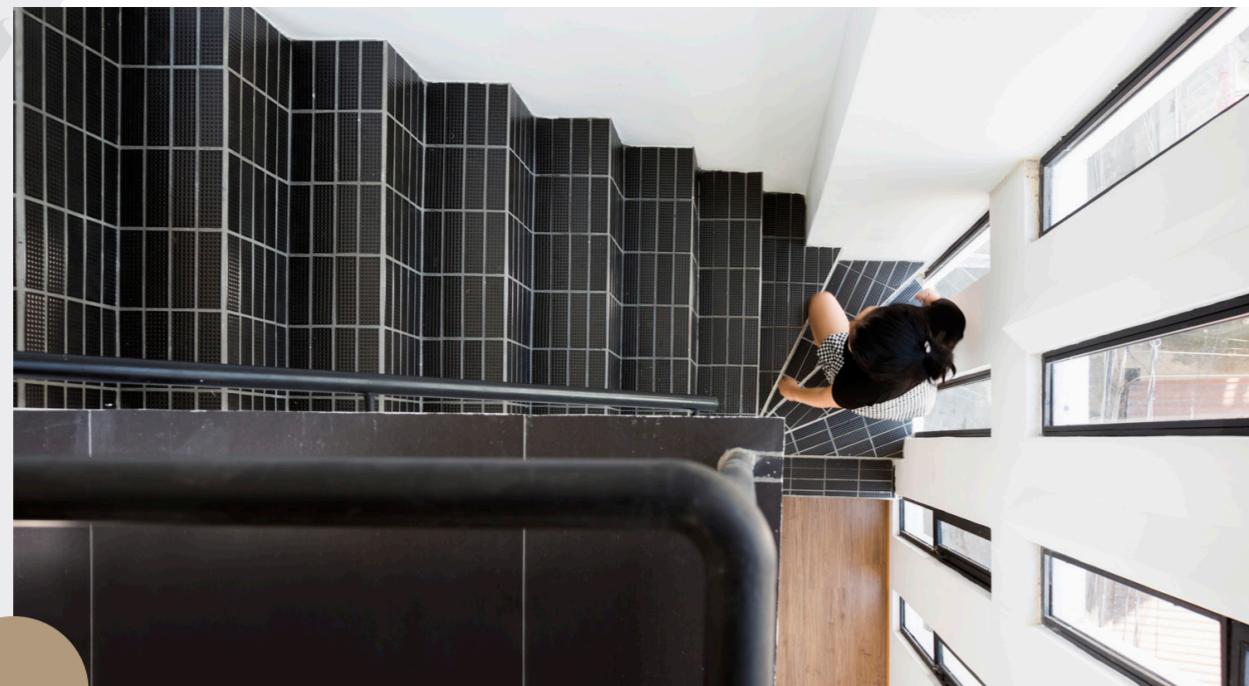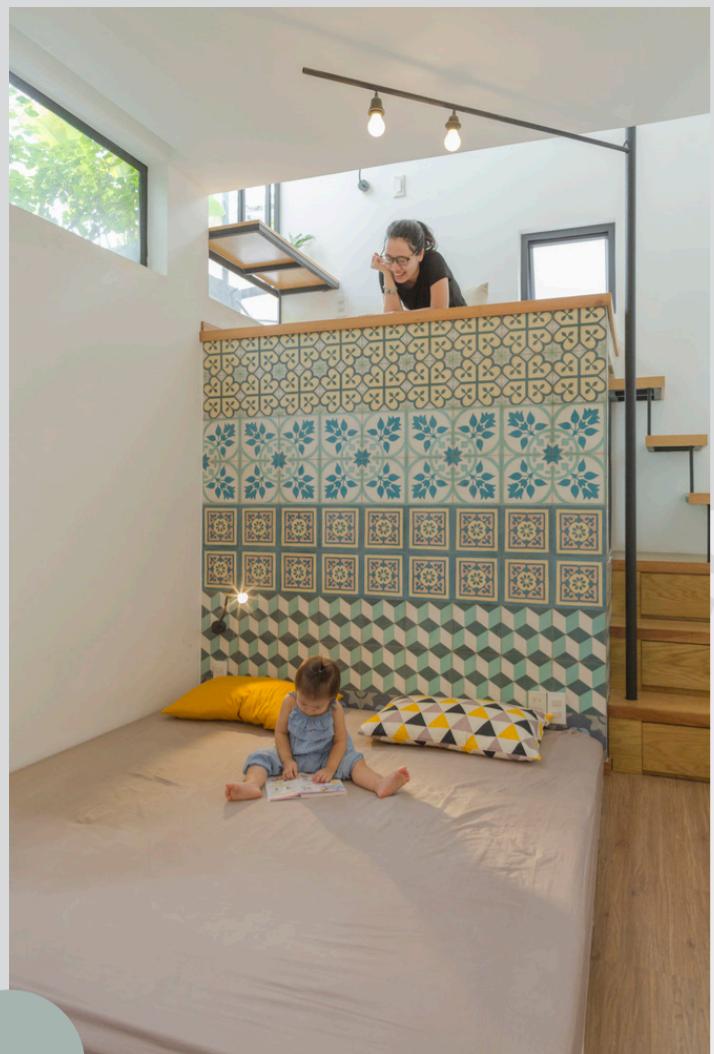


- Toilet
- Future mezzanine
- Bedroom 1
- Bedroom 2
- Worship space
- Reading loft
- Terrace
- Stairs
- Kitchen
- Green

PLANIOMETRY




Ground floor

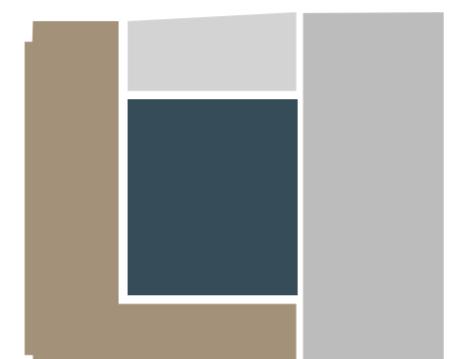

Mezzanine floor




First floor

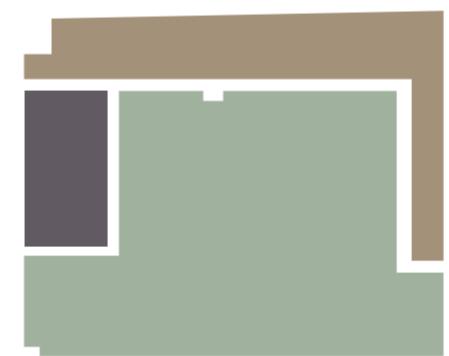


Second floor



Third floor


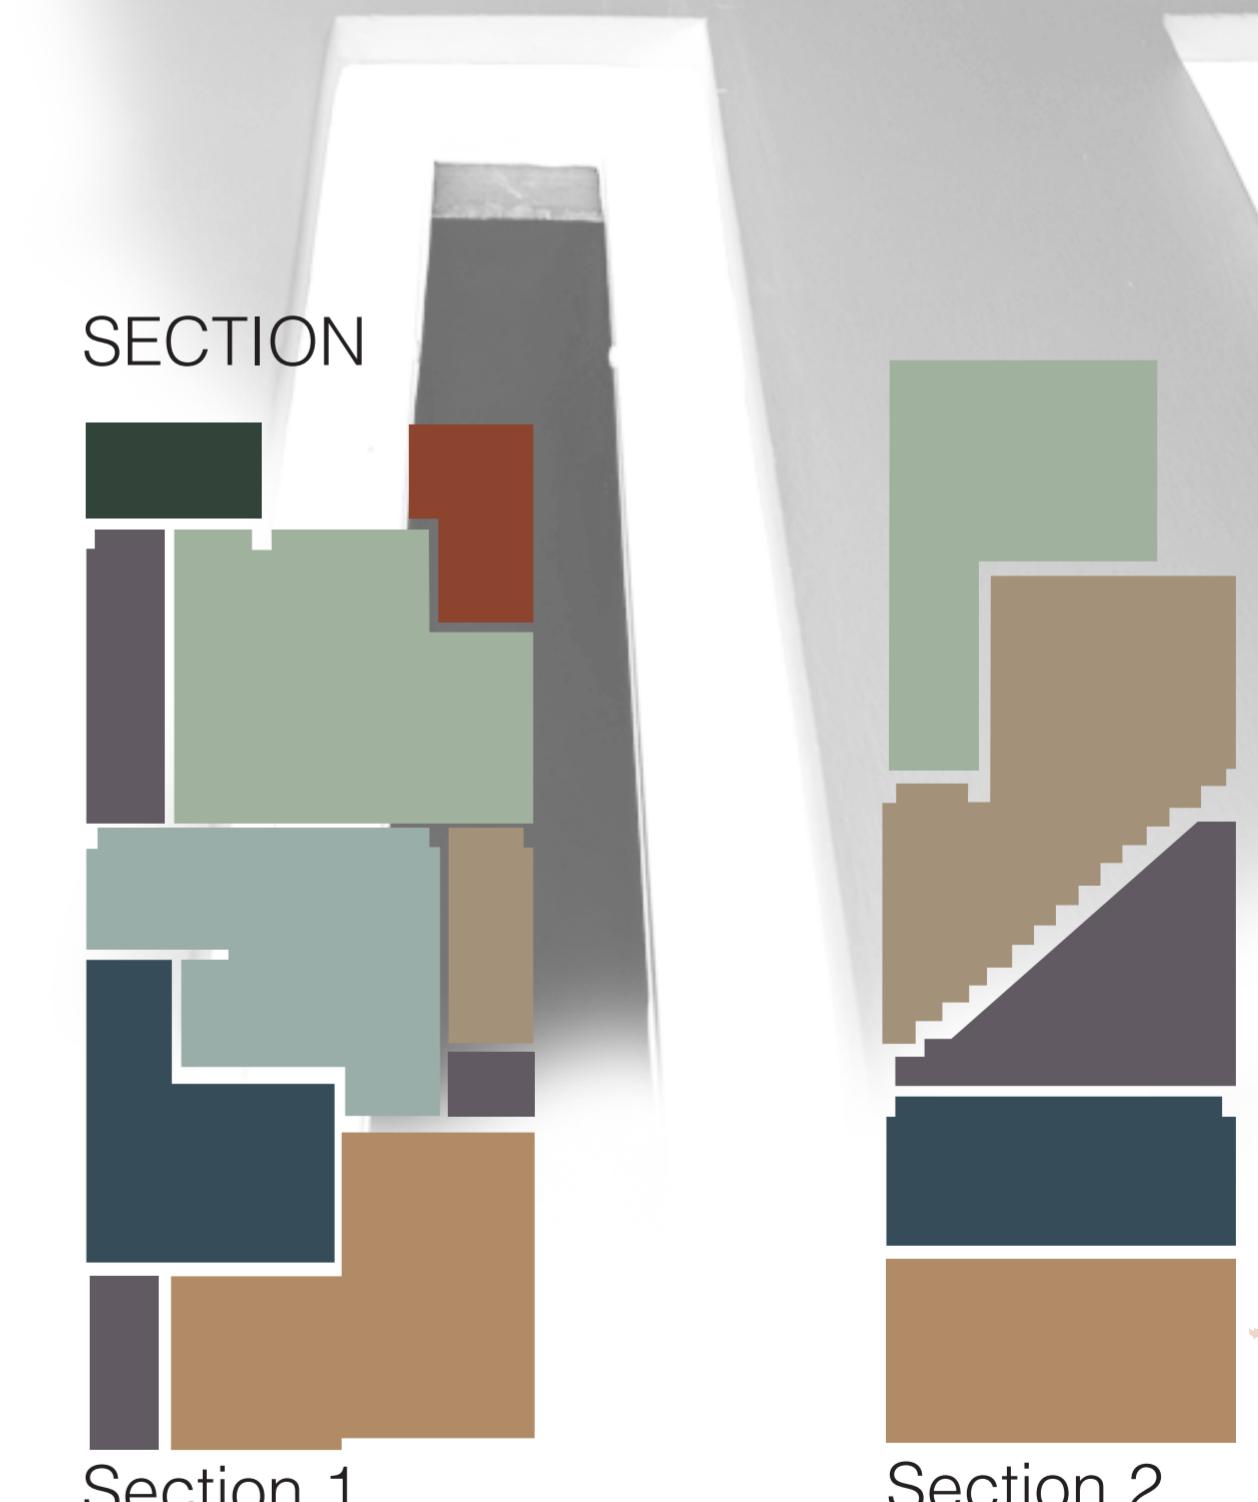


SECTION

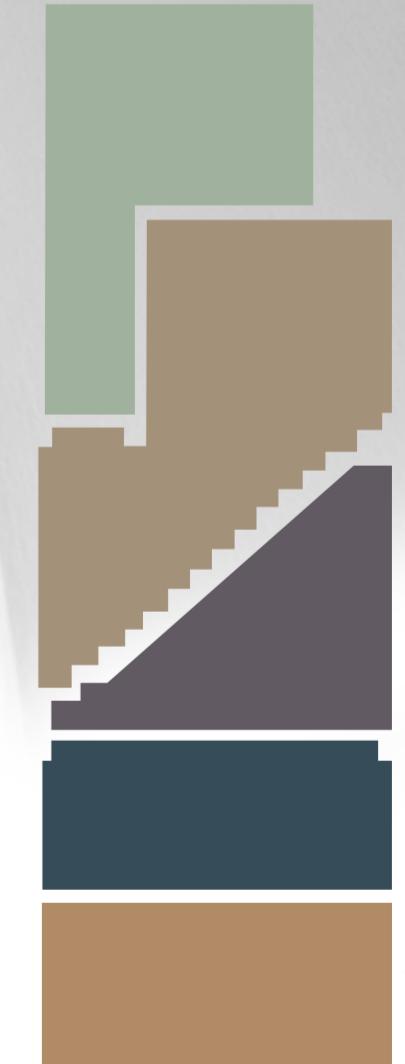

Section 1


Section 2

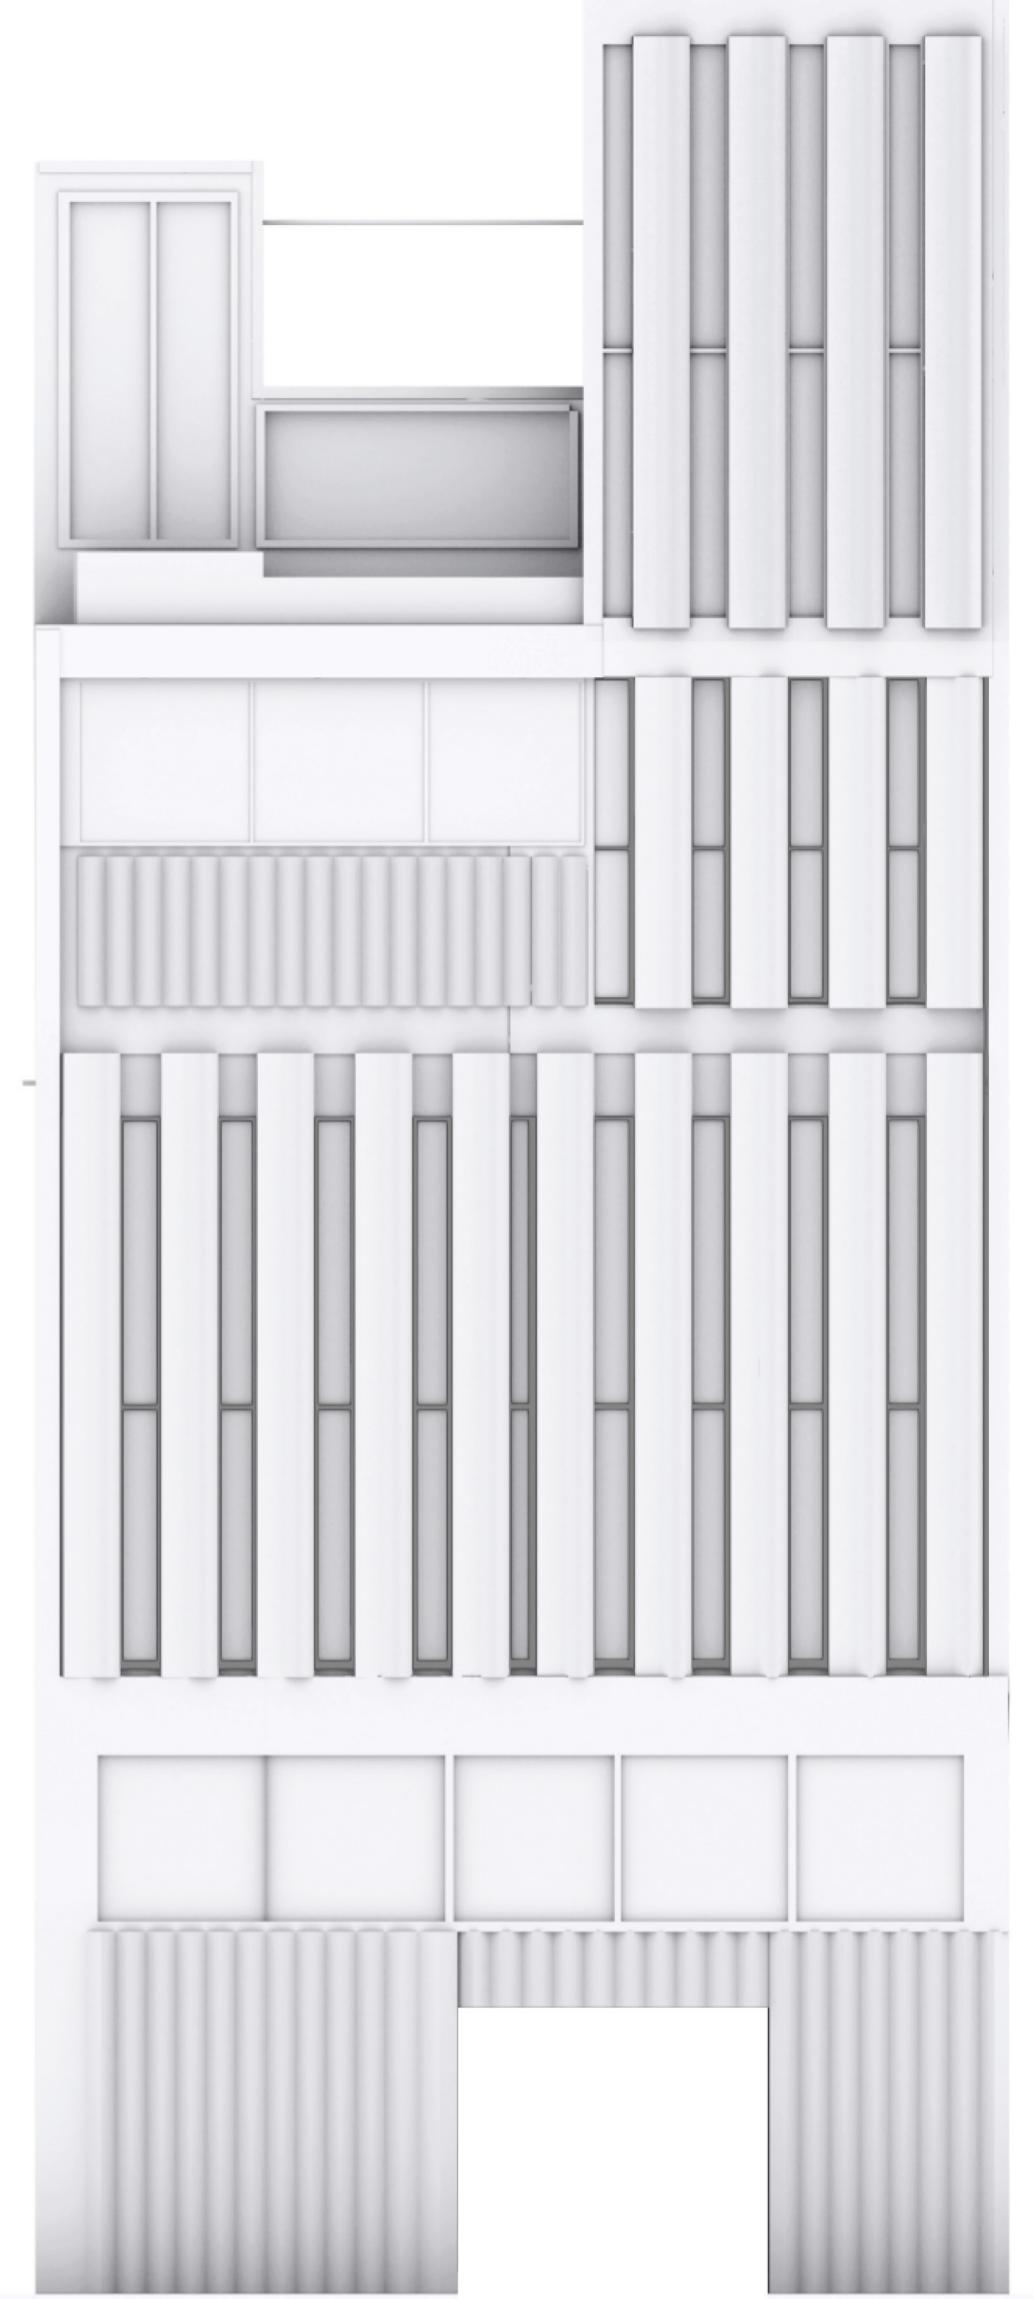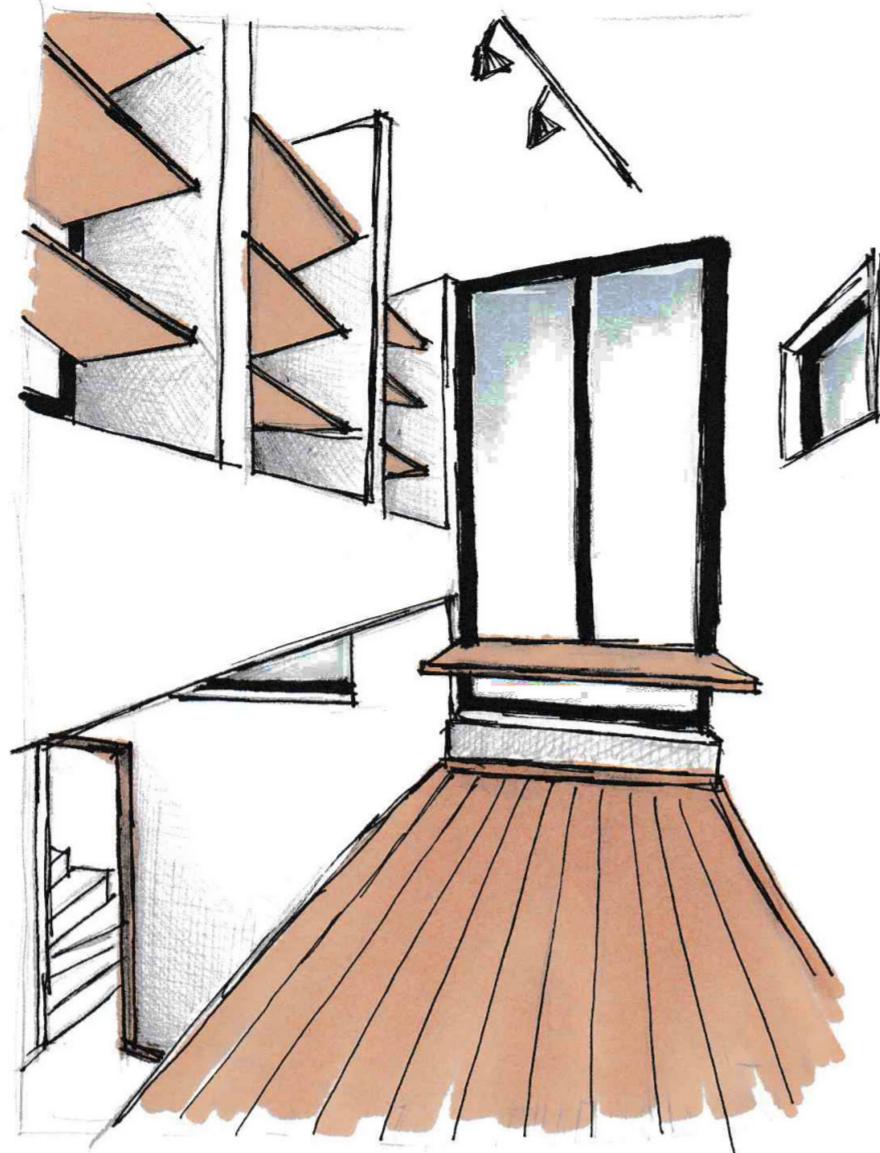

18 House is located in a calm dead-end alley in Ho Chi Minh City, Vietnam.

The plot is a small rectangle of 18 sqm.

The architects worked with a system of a staircase running along the periphery to take advantage of the space underneath for storage cabinets, toilets, and bathrooms. Furthermore, this staircase placement also opened up to a considerably sizeable vertical space for bunk bed or reading loft.

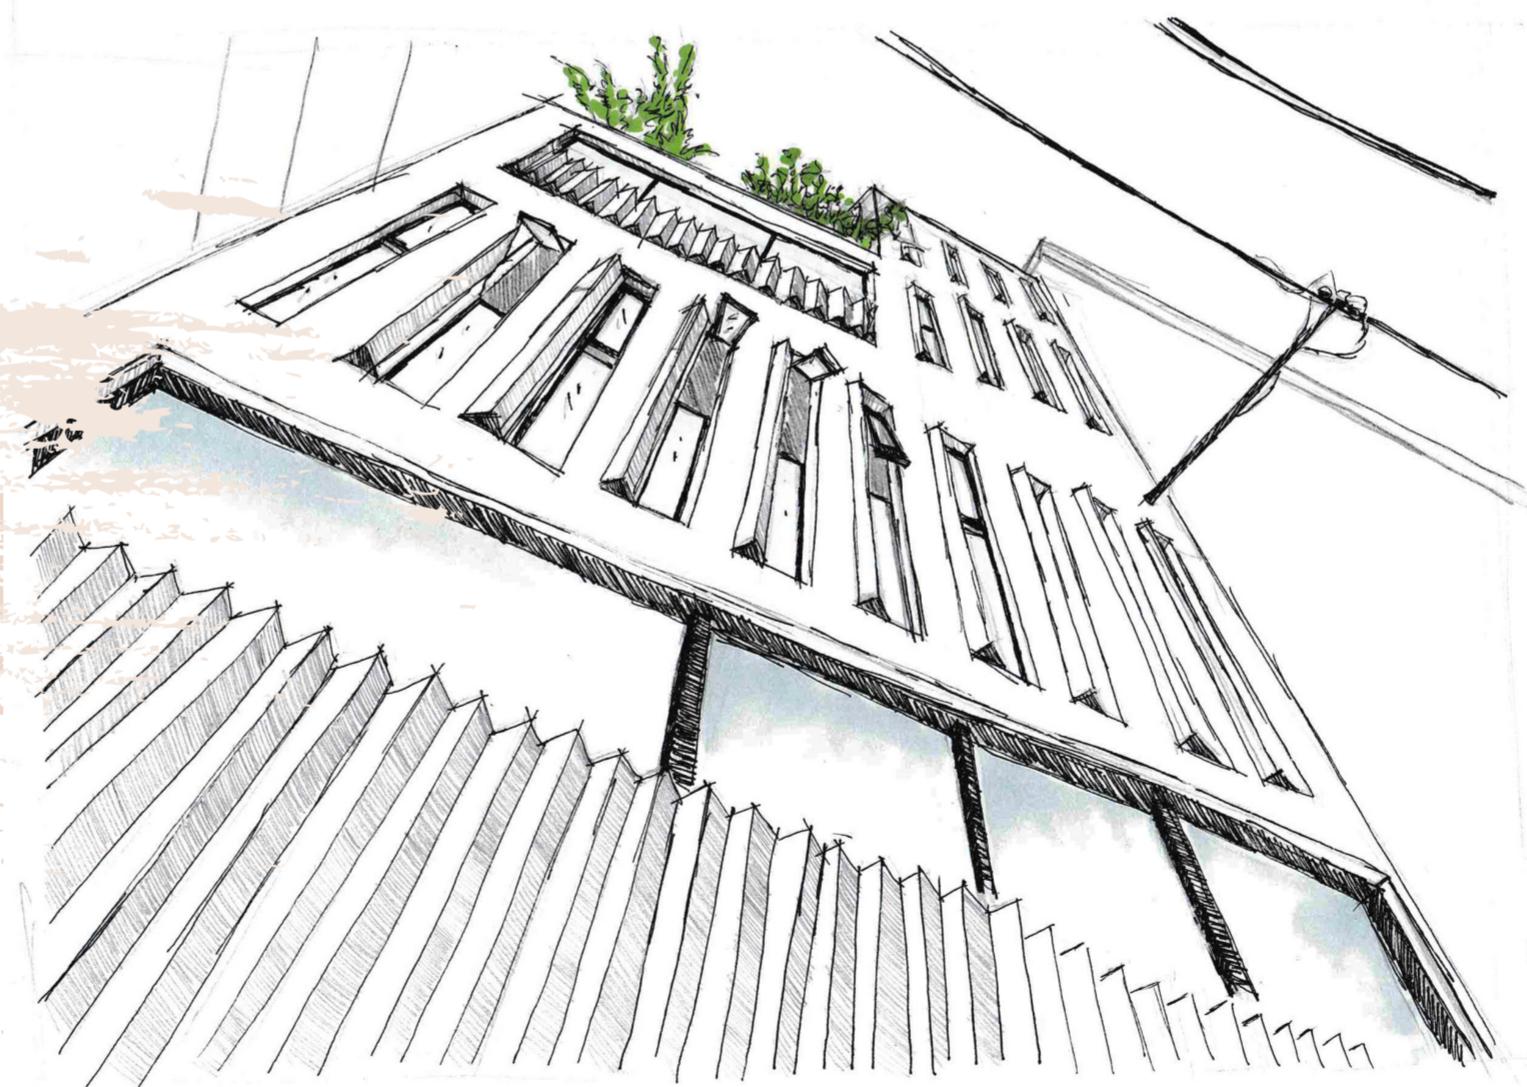

FRONT



POLITECNICO
MILANO 1863

Laboratorio di Modellazione
digitale dello spazio
Anno Accademico
2017-2018

Sezione I5
Docente:
Marco Ferrara


Esame finale
Sara Barilli - 869994
Elisa Lazzarotto -
Giorgia Leone - 878208

03

Despite almost facing a shortage of living space, we still wanted to devote several spots for greeneries to ease off the heavily cramped character of the alley context.

Master bedroom and reading loft are both adorned by a shared plant bed while the rooftop is utilized as a mini veggie garden.


The architectural envelope facing the alley is comprised of a system of slits with various heights which can be operated separately. This means the users can very well control the ventilation level of the house by selecting a specific number of windows to open.

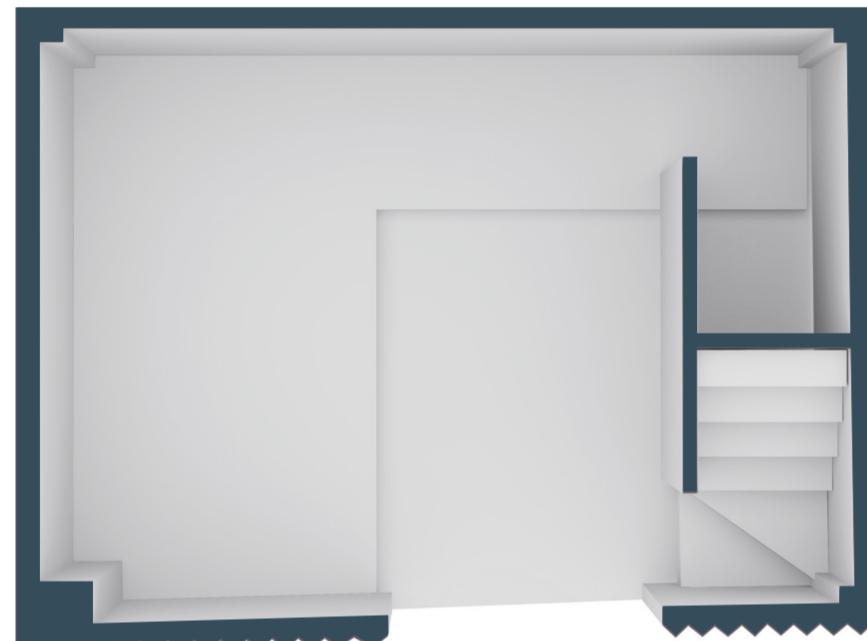

GROUND FLOOR



SECOND FLOOR

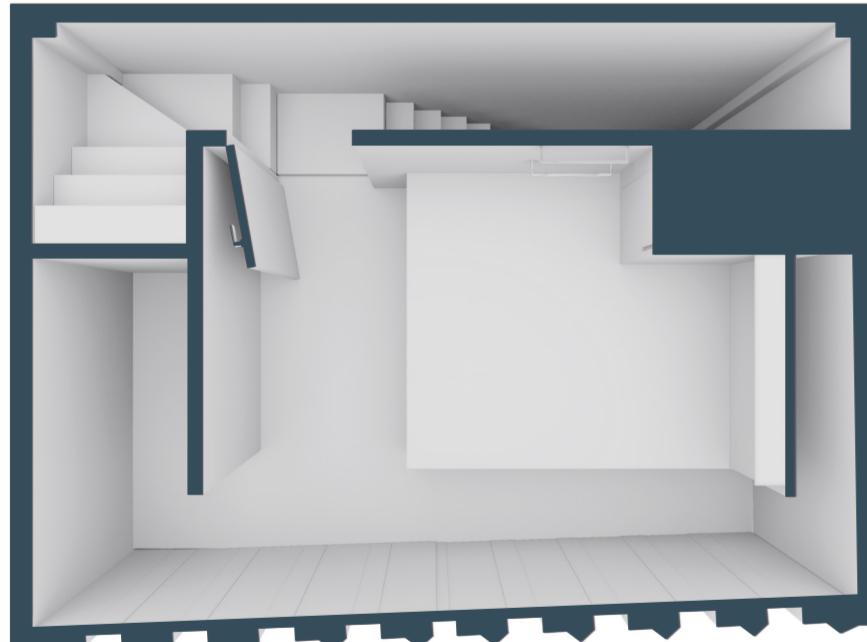

FIRST FLOOR




THIRD FLOOR



SECTION

KITCHEN

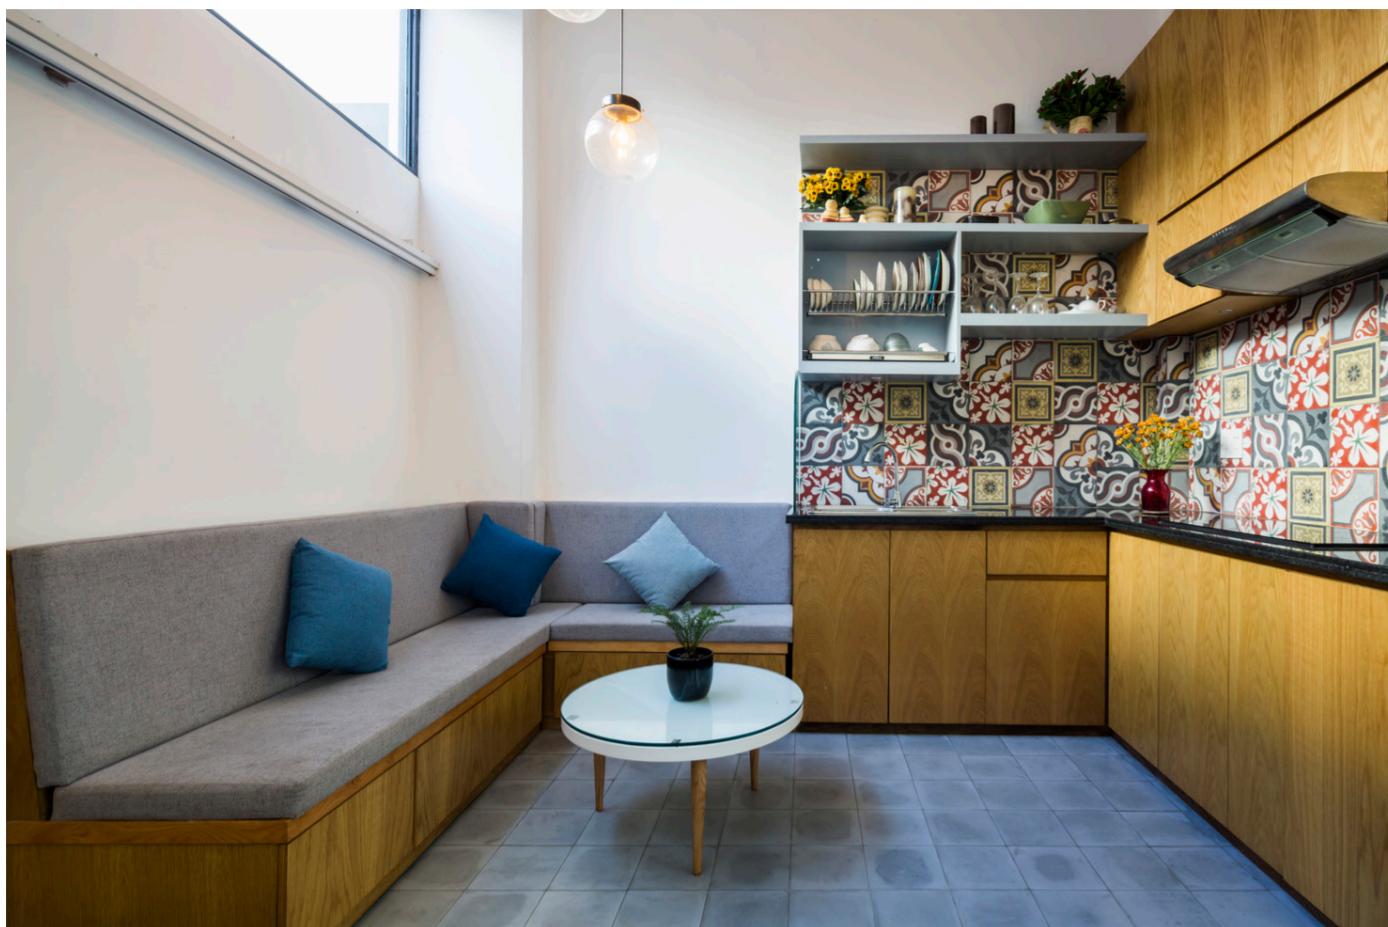

BEDROOM



POLITECNICO
MILANO 1863

Laboratorio di Modellazione
digitale dello spazio
Anno Accademico
2017-2018

Sezione I5
Docente:
Marco Ferrara

Esame finale
Sara Barilli - 869994
Elisa Lazzarotto -
Giorgia Leone - 878208

05