

WHITE CUBE HOUSE

MM++ Architects

DOVE // Ho Chi Minh City, Vietnam

ARCHITETTI IN CARICA // My An Pham Thi, Michael Charrault


ANNO DI PROGETTO // 2016

L'edificio si trova in una zona residenziale nel distretto 7 della città di Ho Chi Minh e ospita una coppia con 2 bambini piccoli. Il terreno è un quadrato di 15 metri di lunghezza. L'orientamento della casa, il clima e l'ambiente circostante hanno portato alla progettazione delle elevazioni con soluzioni minimaliste ma efficaci. La casa è divisa in 3 blocchi distinti.


L'ingombro del piano terra è impostato per mantenere intatta la forma del riquadro bianco superiore. È uno spazio aperto che unisce la cucina con la sala da pranzo e il soggiorno. È completamente vetrato sul lato est, parzialmente sui lati Nord e Sud, aprendosi sul giardino. La grande cornice di vetro lungo la scala che è dotata di un parasole automatico per controllare la quantità di luce del sole nel pomeriggio.

Il cubo bianco al primo piano è il volume principale della costruzione. Ospita 2 camere da letto con bagno e un ampio soppalco lungo la scala. In contrasto con il piano terra, è un blocco solido con muri spessi in doppio mattone isolati per mantenere la casa fresca. 2 logge profonde con fioriere incorporate sono collocate a sud e ad est della costruzione: la fitta vegetazione aiuta a controllare le viste e porta privacy. Sul soppalco, una seconda scala a chiocciola conduce al piano superiore.


Il secondo piano è il terzo volume separato incassato, posto sul cubo bianco. Tetto e pareti inclinate sono ricoperte da piastrelle in ardesia. Uno strato isolante sopra il telaio in cemento mantiene questo pavimento fresco nonostante sia esposto al calore del sole tutto il giorno. Le fioriere integrate con vegetazione aiutano a filtrare la luce diretta del sole e controllano le viste. Il bagno principale e il salotto si aprono su una terrazza sul lato est.

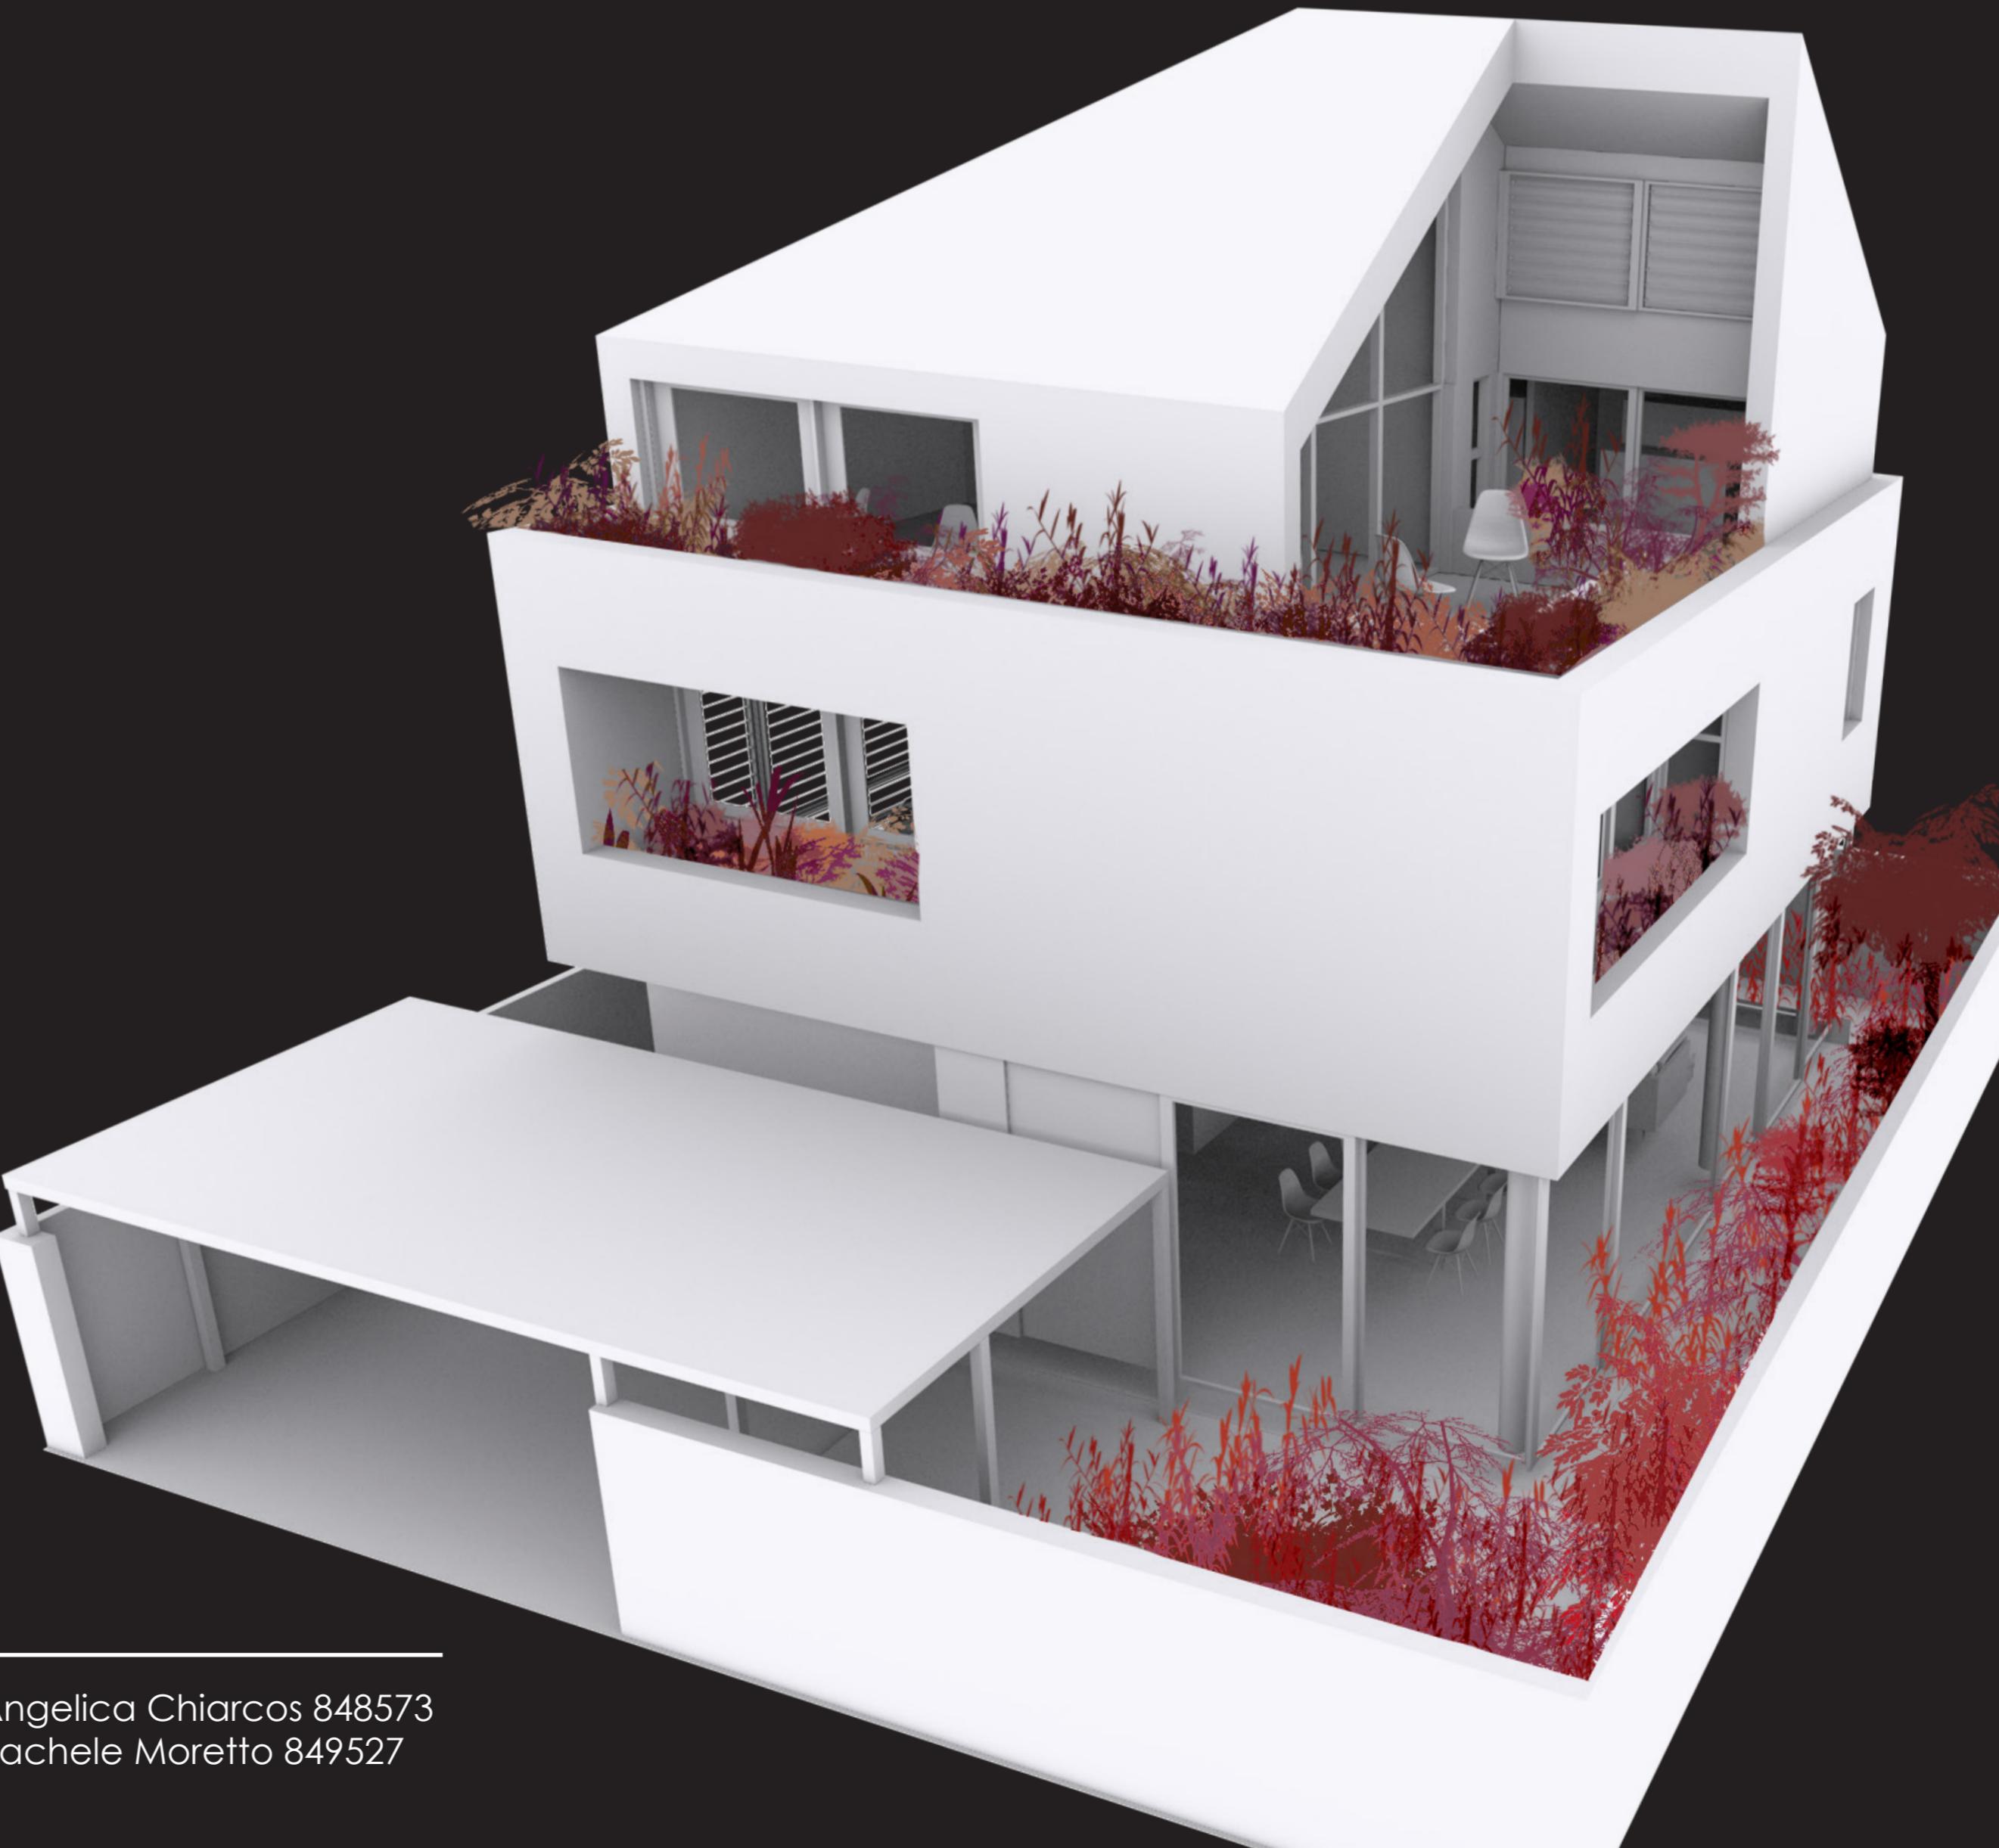

PIANTE E SEZIONI //

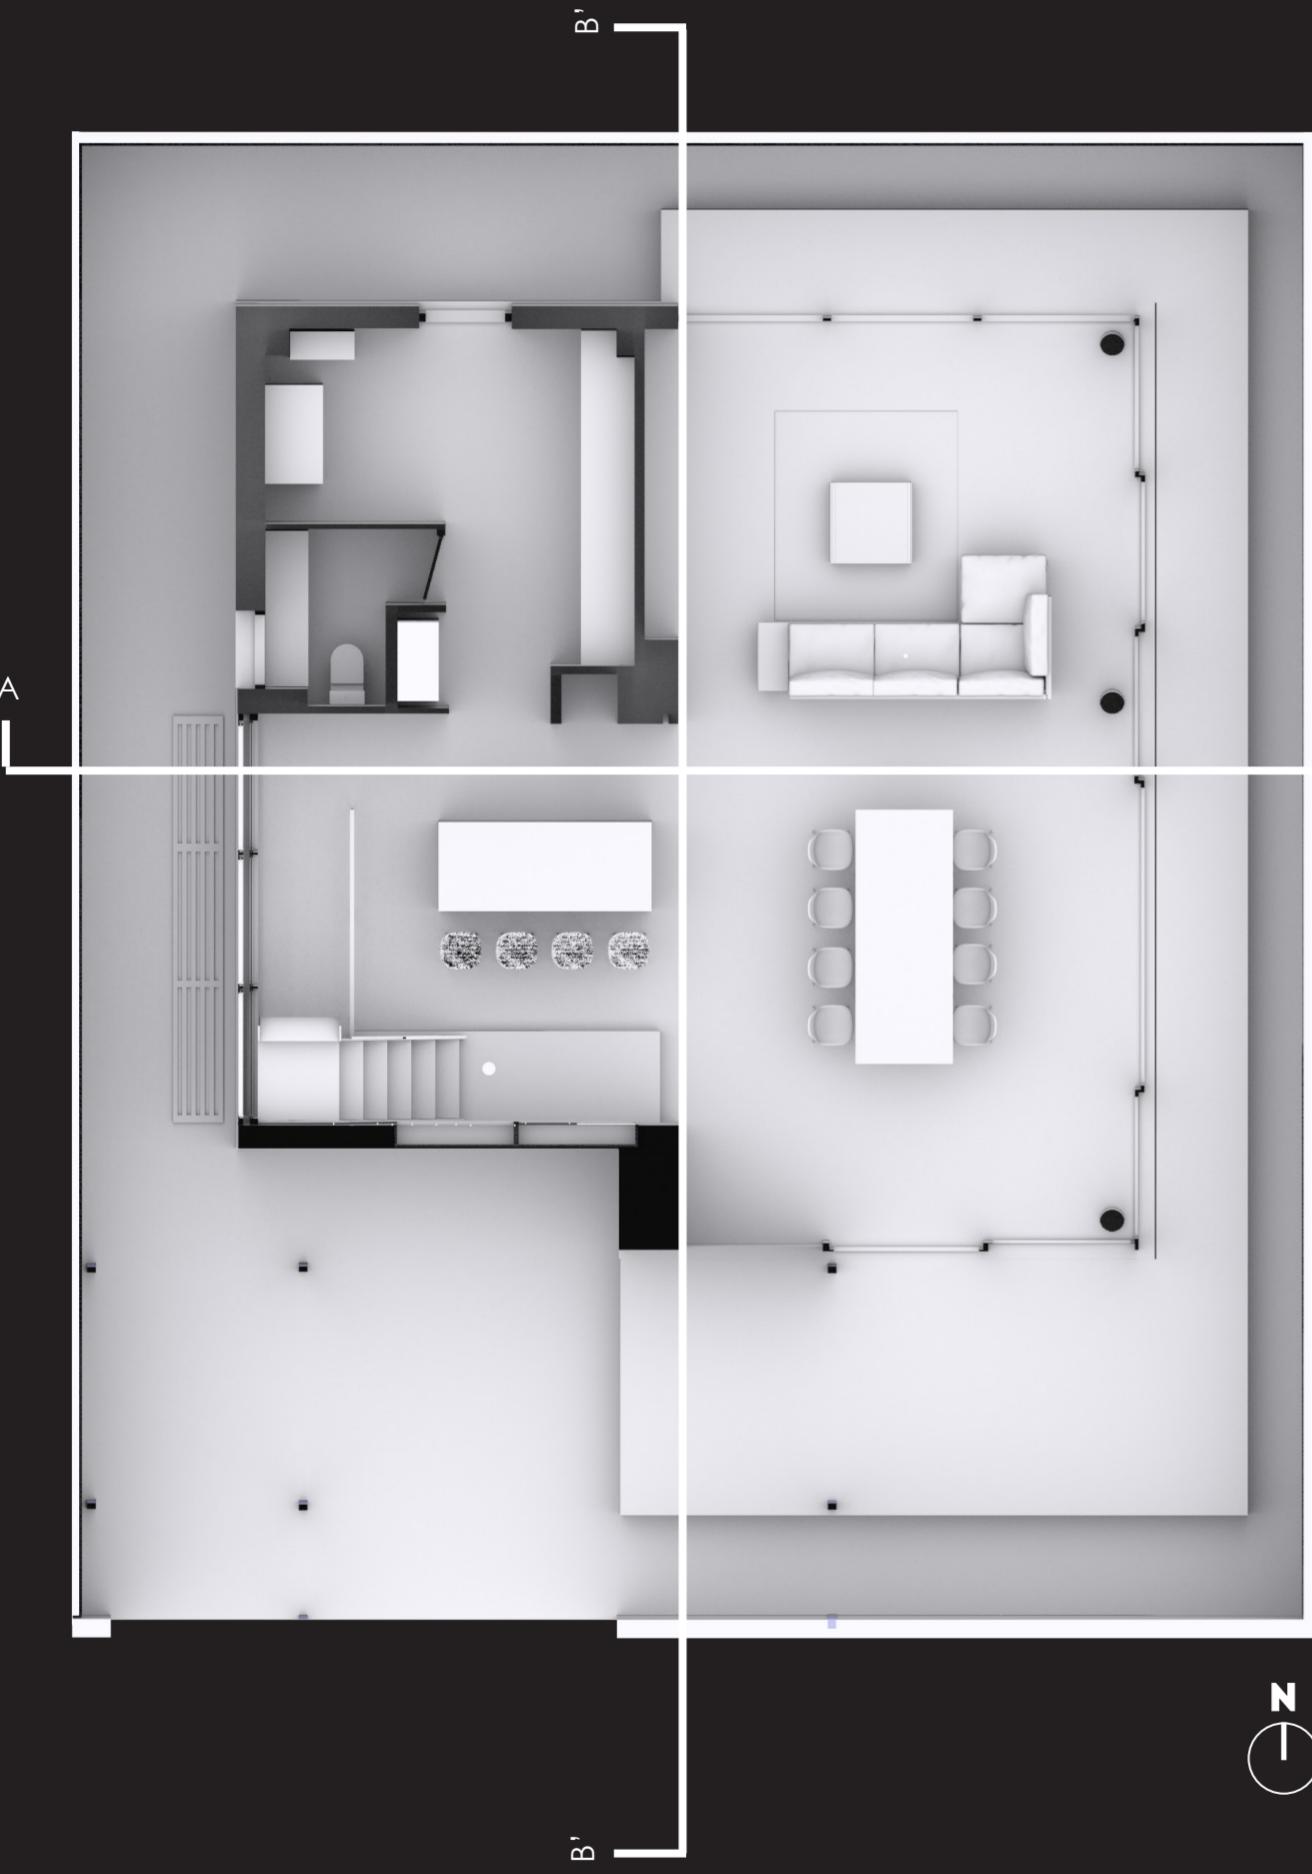

PIANO TERRA

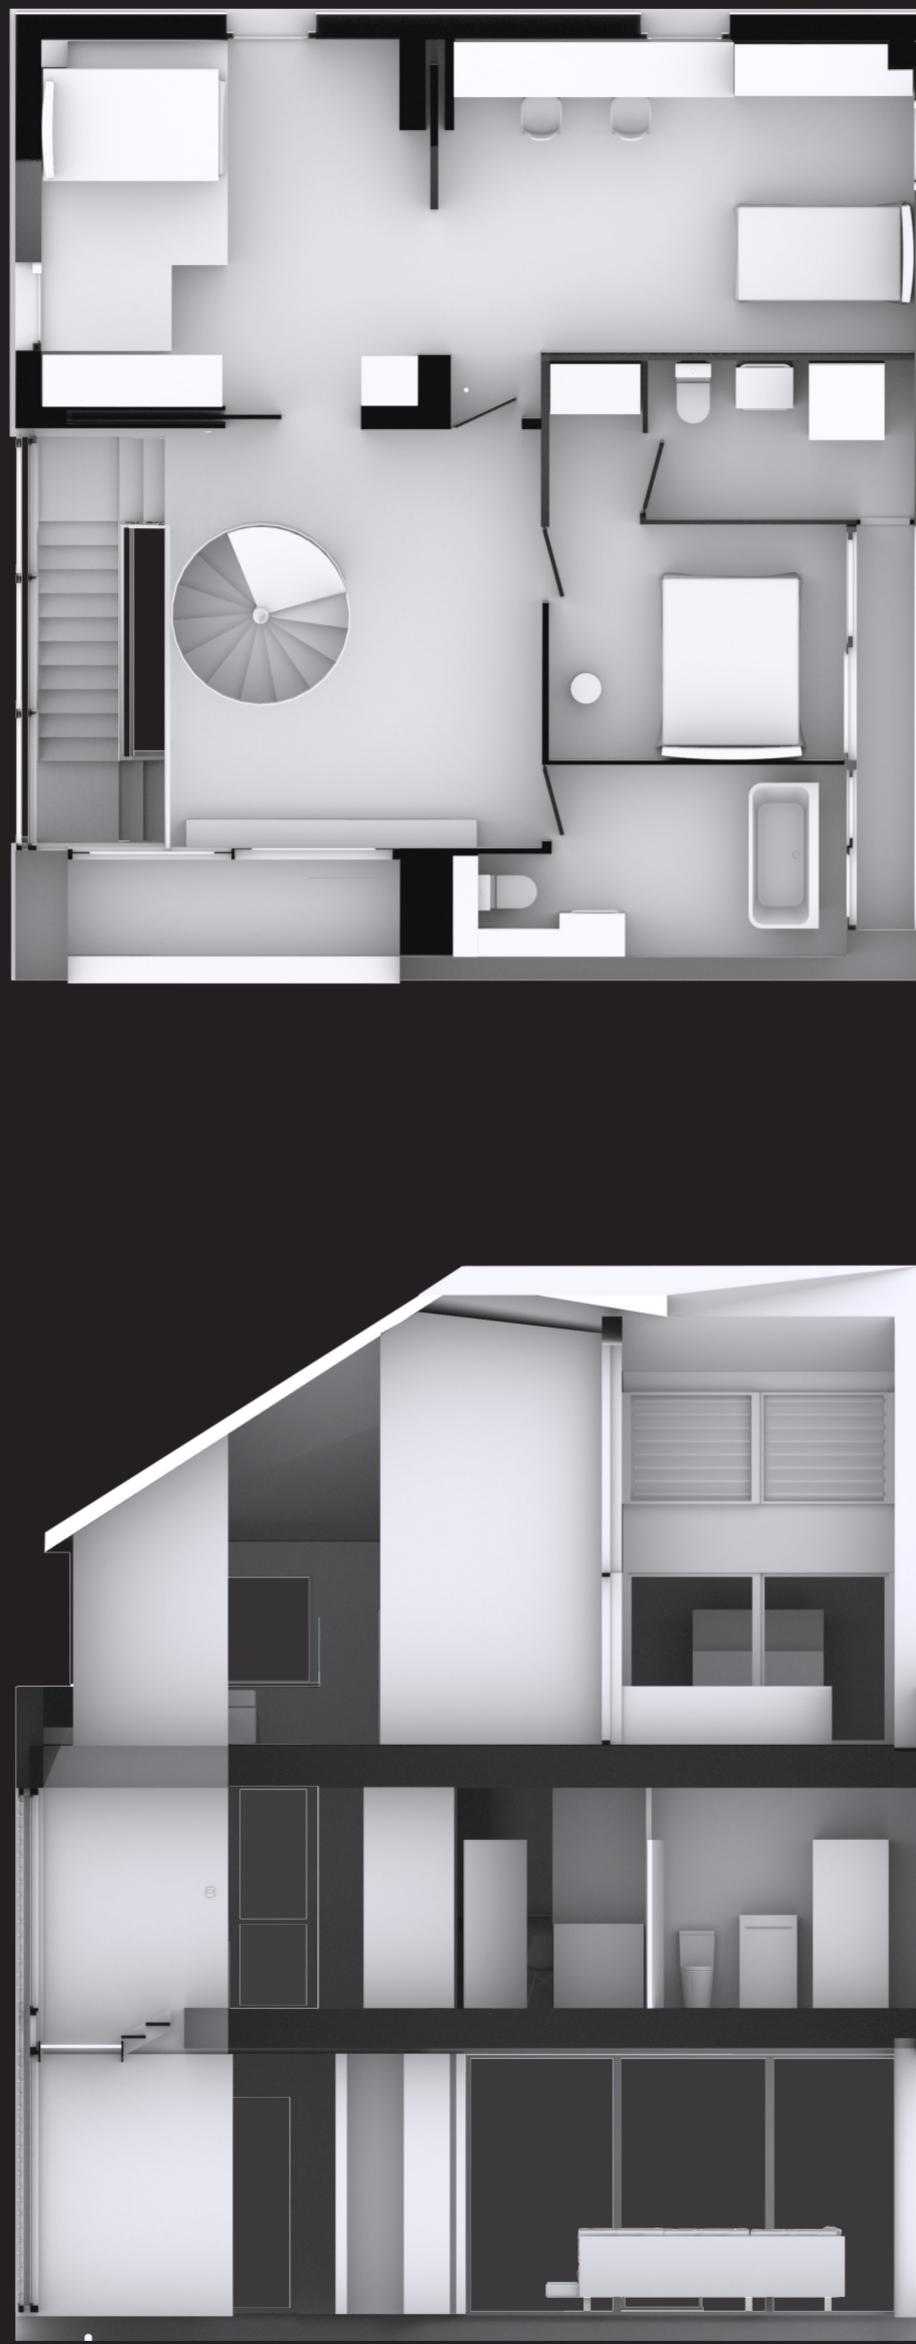

PRIMO PIANO



SECONDO PIANO





SEZIONE A - A'




SEZIONE B - B'

PROSPETTI //

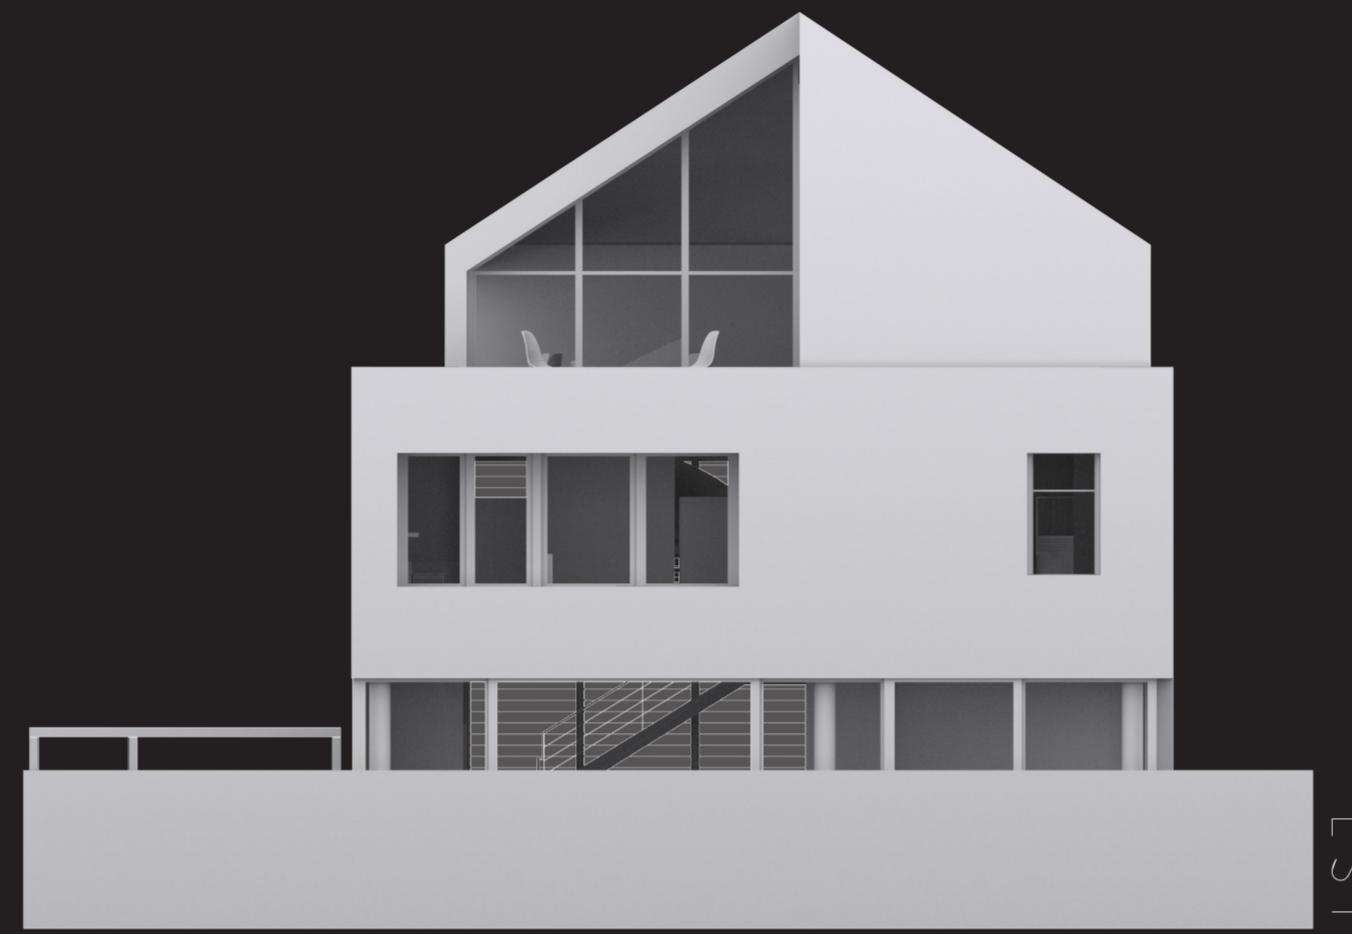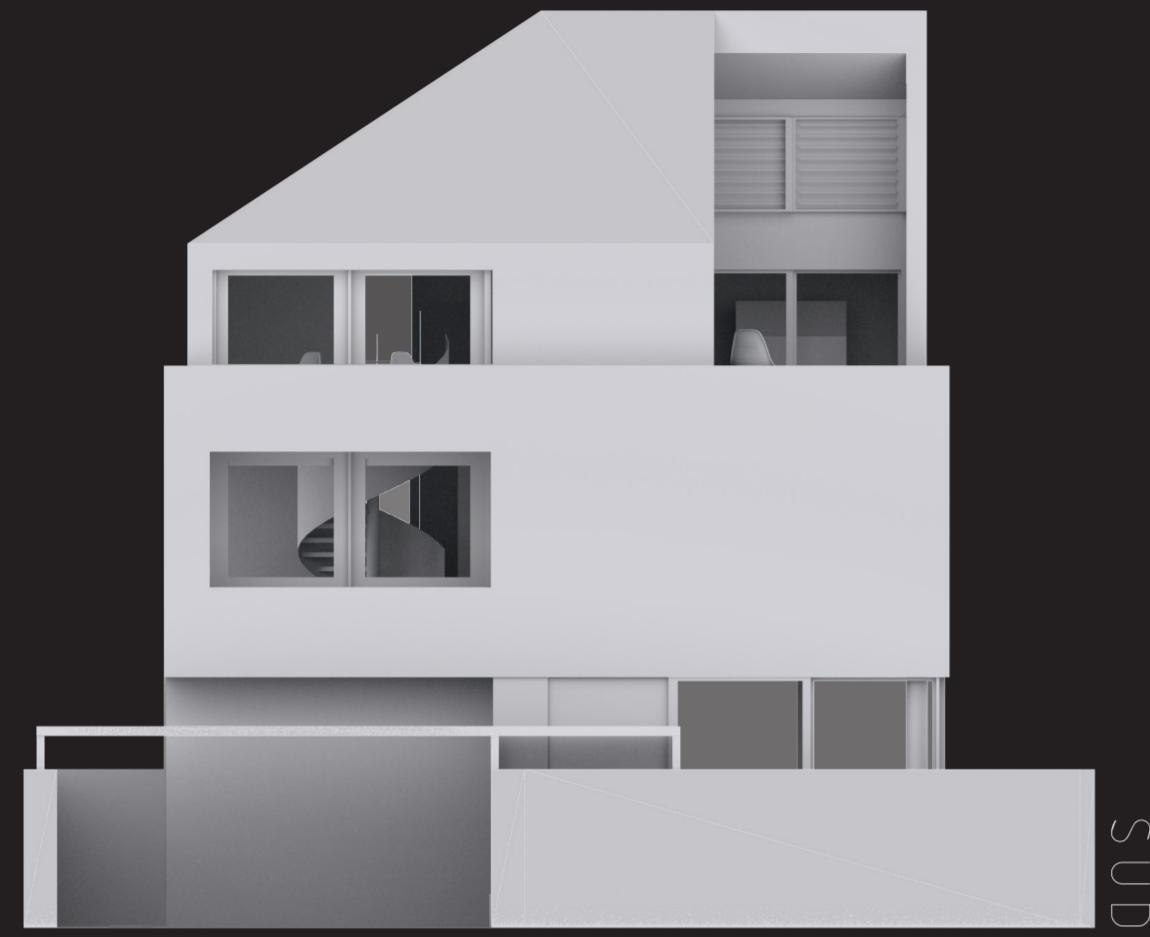

ASSONOMETRIE
OMBREGGIATE //

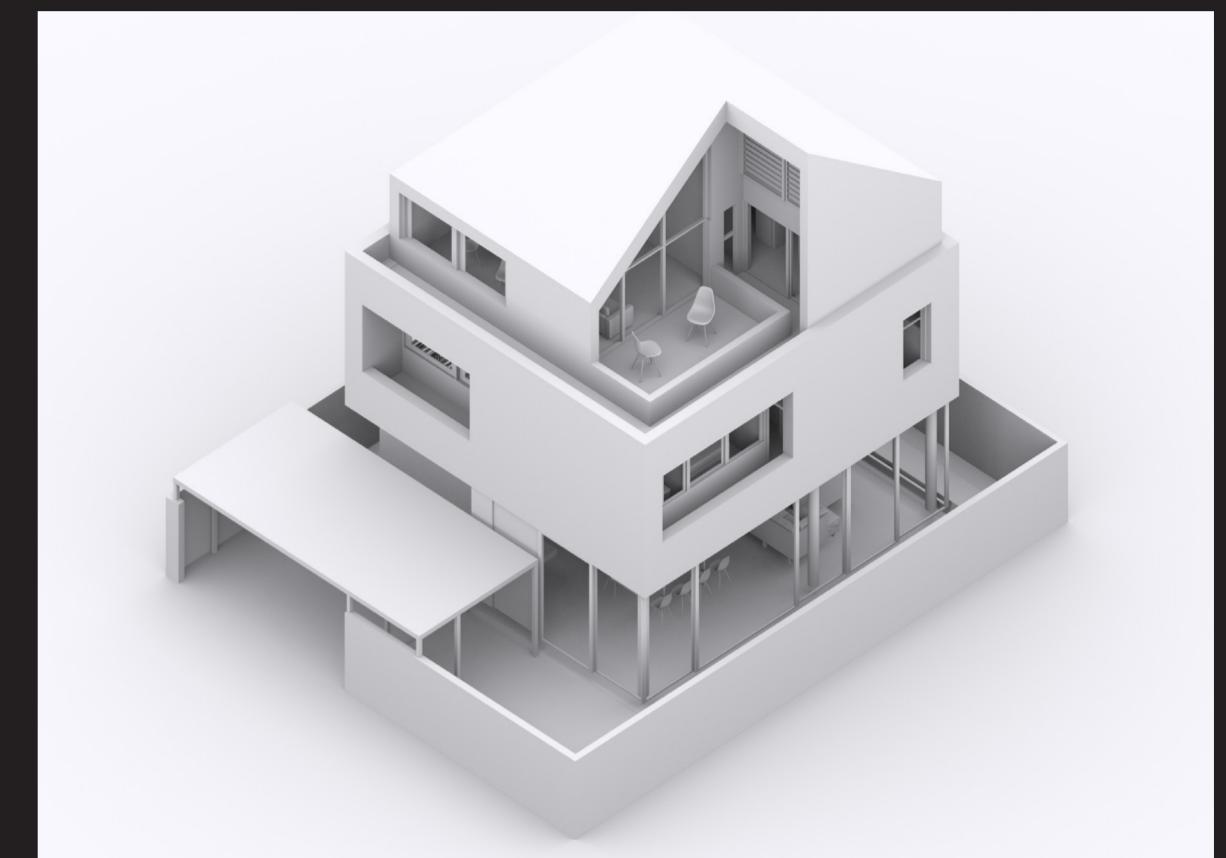

VISTE WIREFRAME //



PROSPETTIVE //

