

# BRICK HOUSE - BASTIAN ARCHITECTURE

## INFORMATIONS


**Architects:**  
Bastian Architecture  
**Location:**  
Annandale, Australia  
**Area:**  
79.0 m<sup>2</sup>  
**Project Year:**  
2015  
**Manufacturers:**  
Ceasarstone  
**Builder:**  
Laycock Constructions  
**Structural Engineer:**  
SDA Structures




## THE PROJECT

This project saw the revitalisation of an inner city worker's cottage. The renovation opened up the internal spaces, provided natural light and a direct connection to the outdoor area. The renovations took cue from this wall, utilizing a variety of bricks throughout the extension. New bricks weave through the project, beginning inside as the kitchen bench, wrapping along the length of the room as a ledge for artwork + modern essentials, snaking outside and bulging to form a BBQ bench before finally dipping down to create a long bench seat.

## PLAN

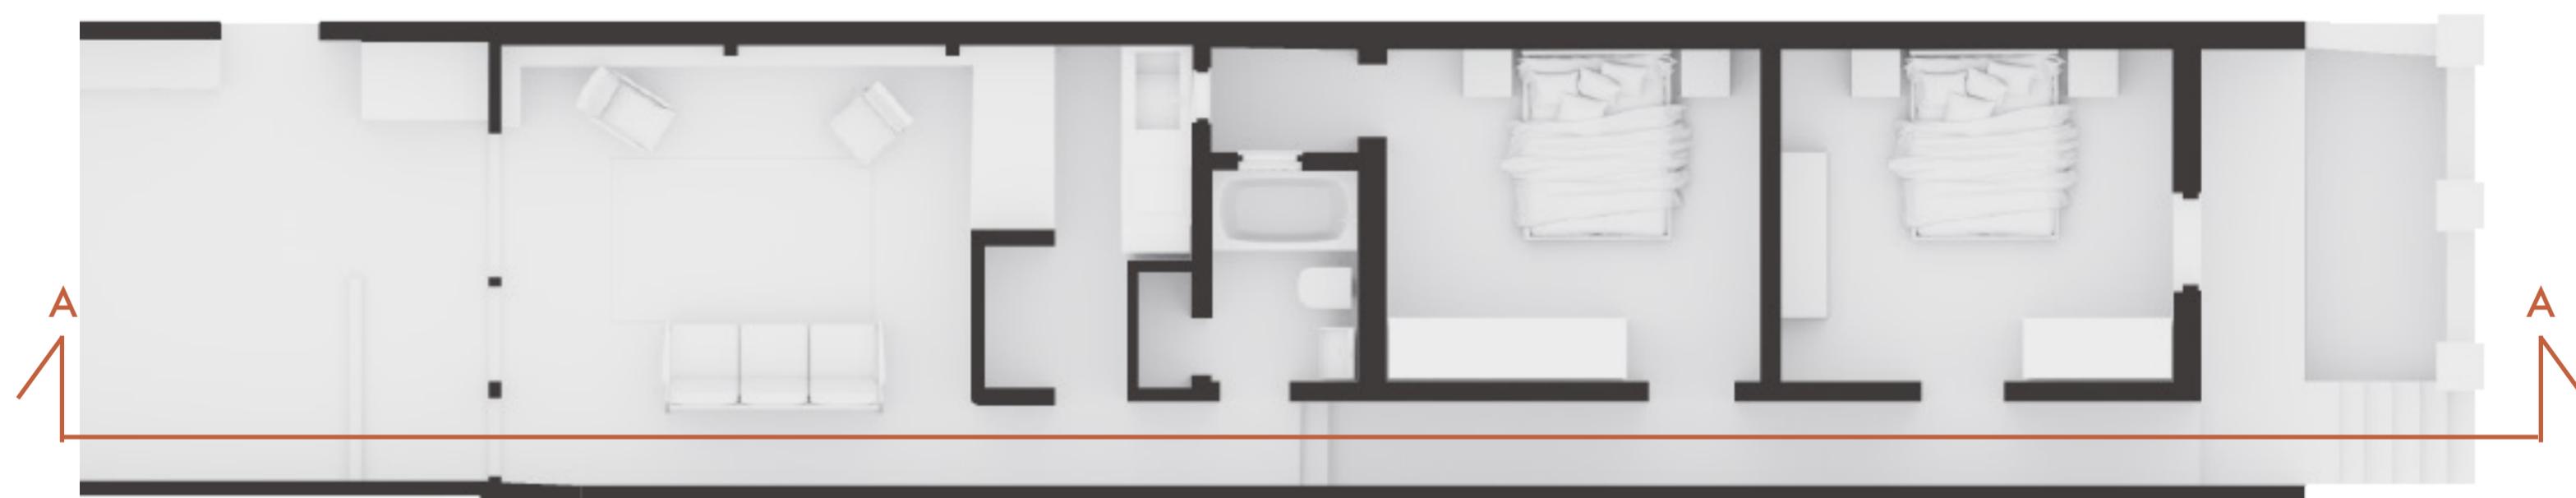

## SECTION A-A

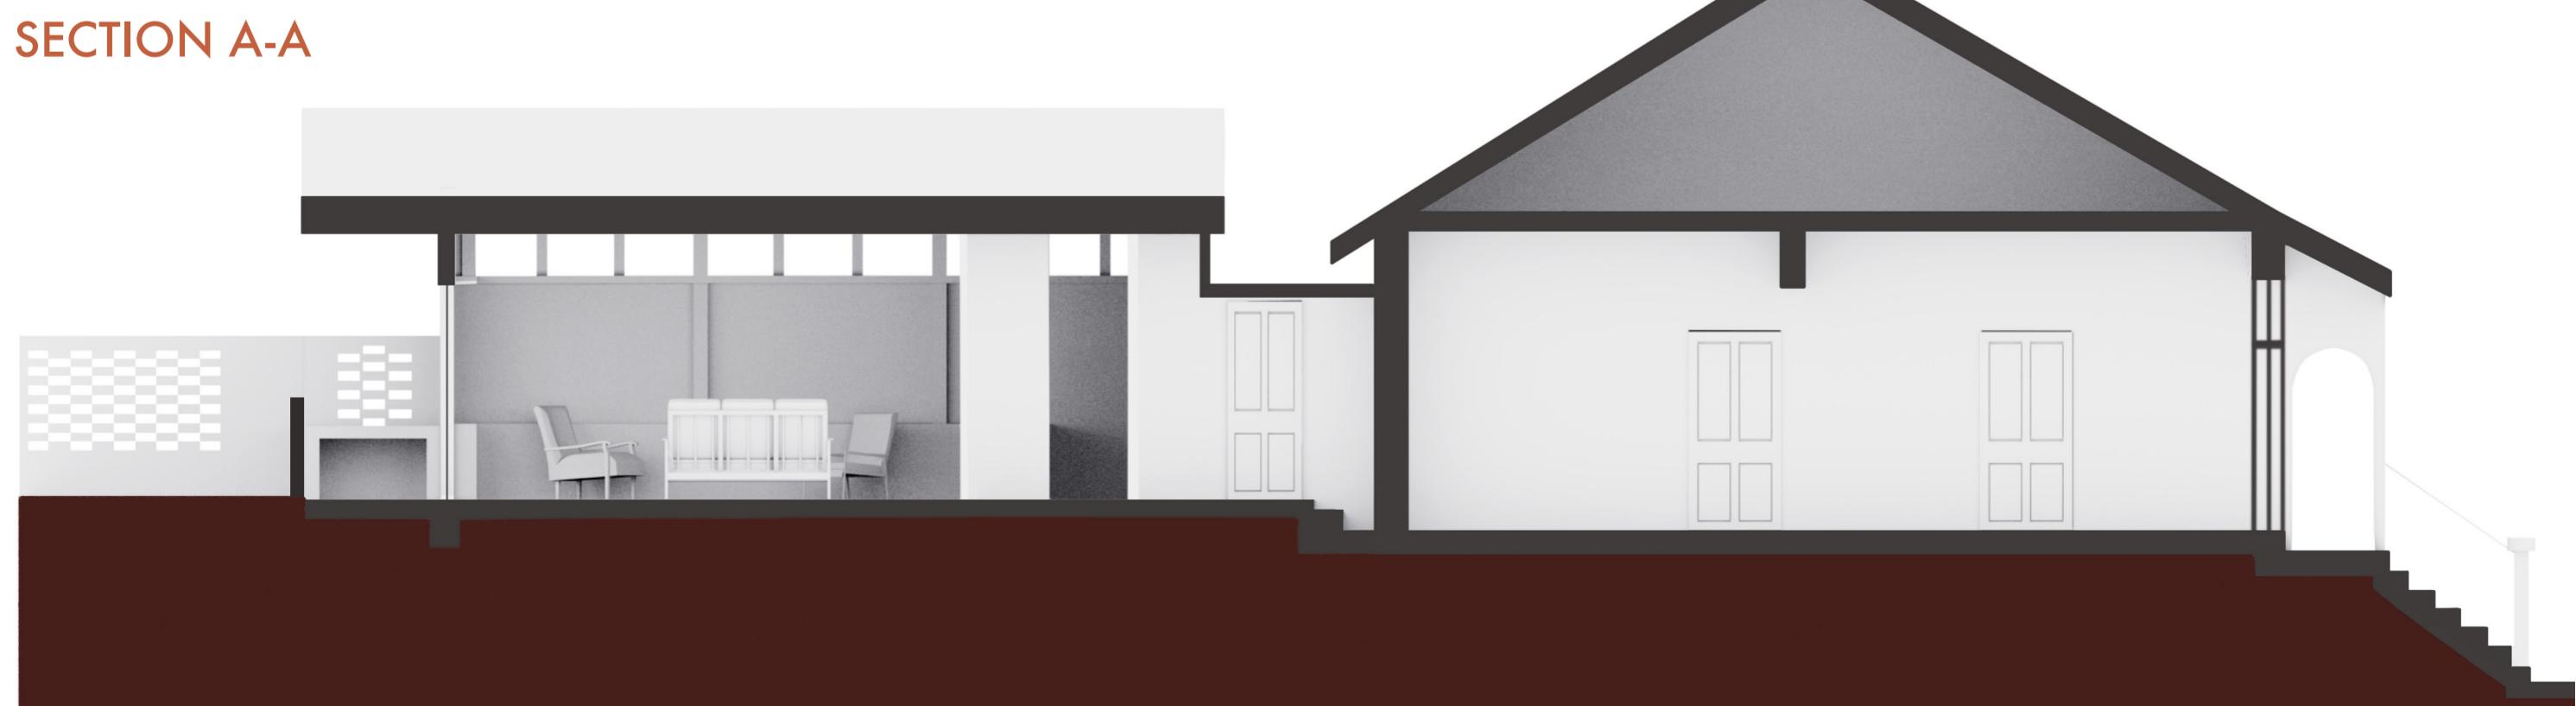

## THE INTERIORS

Recycled bricks sourced extended the remnant wall, adding texture and colour in an otherwise monochrome extension. The materiality of the bricks is contrasted by a folded white living/kitchen/dining space. The roof folds up to North providing light + ventilation while creating a sense of weightlessness which counteracts the solid brick base.

## BATHROOM



## LIVING



## KITCHEN

