


# KARELIAN HOUSE

Architects: Drozdov & Partners


Location: Saint Petersburg, Russia

Project year: 2017


Area: 300m<sup>2</sup>

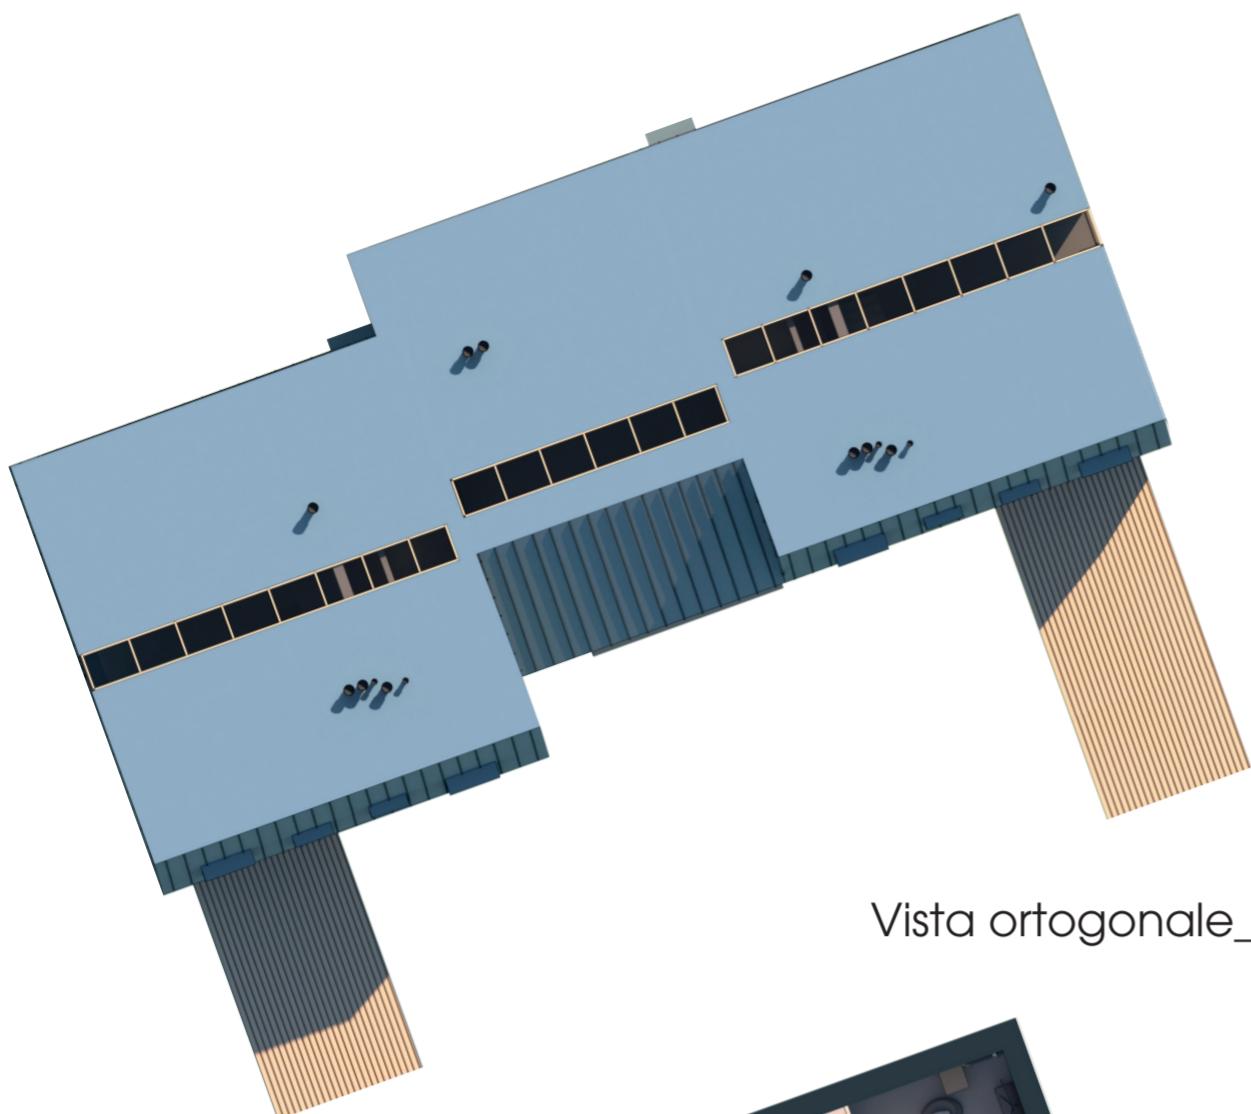

Vista ortogonale\_Tetto

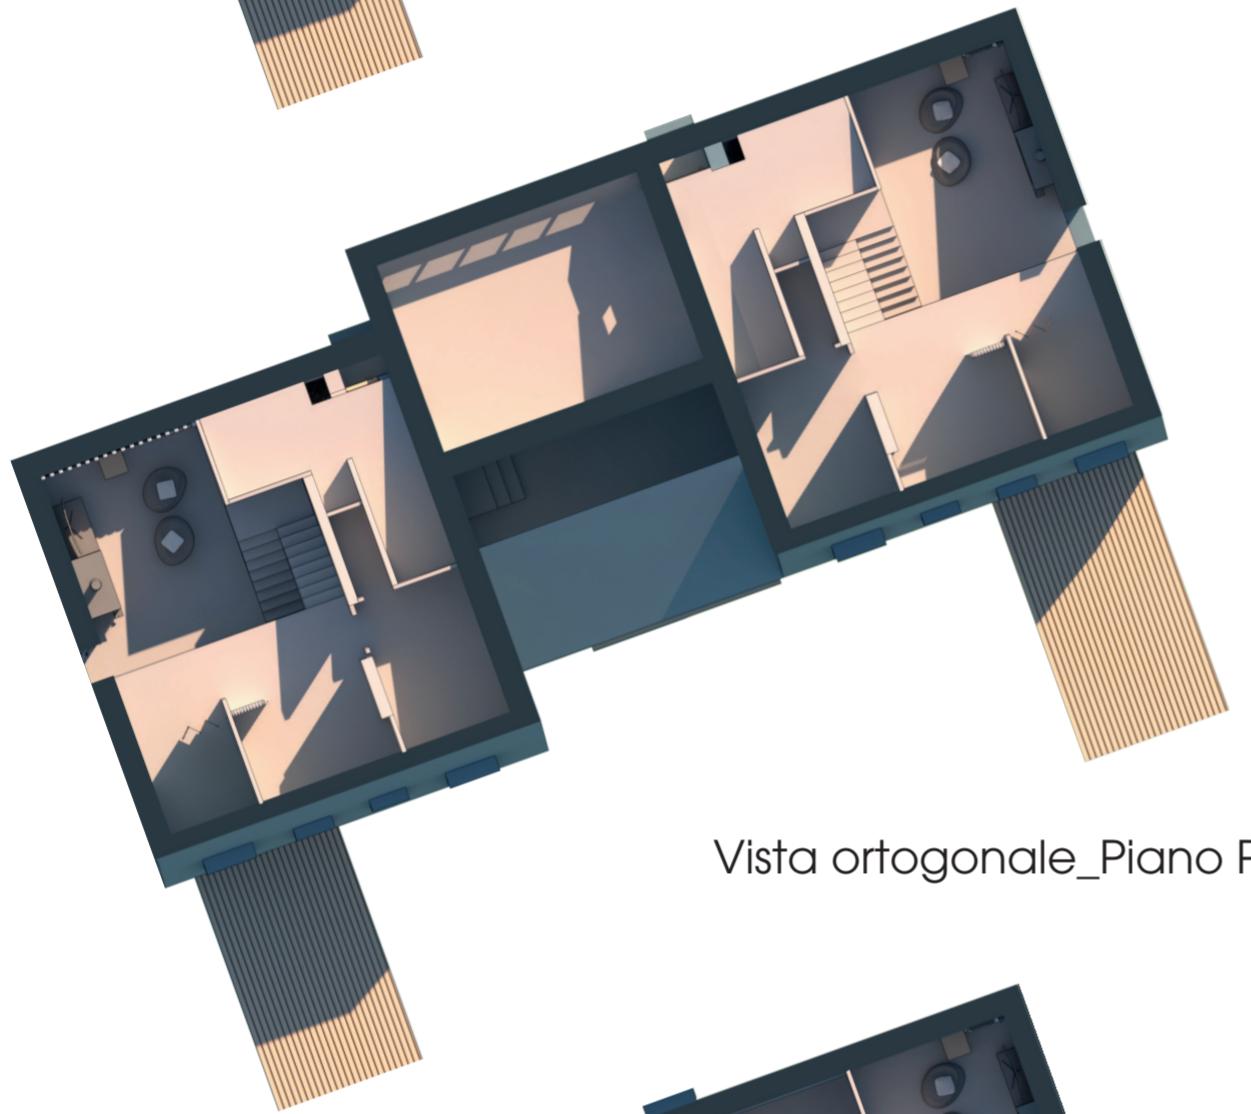

Vista ortogonale\_Piano Primo

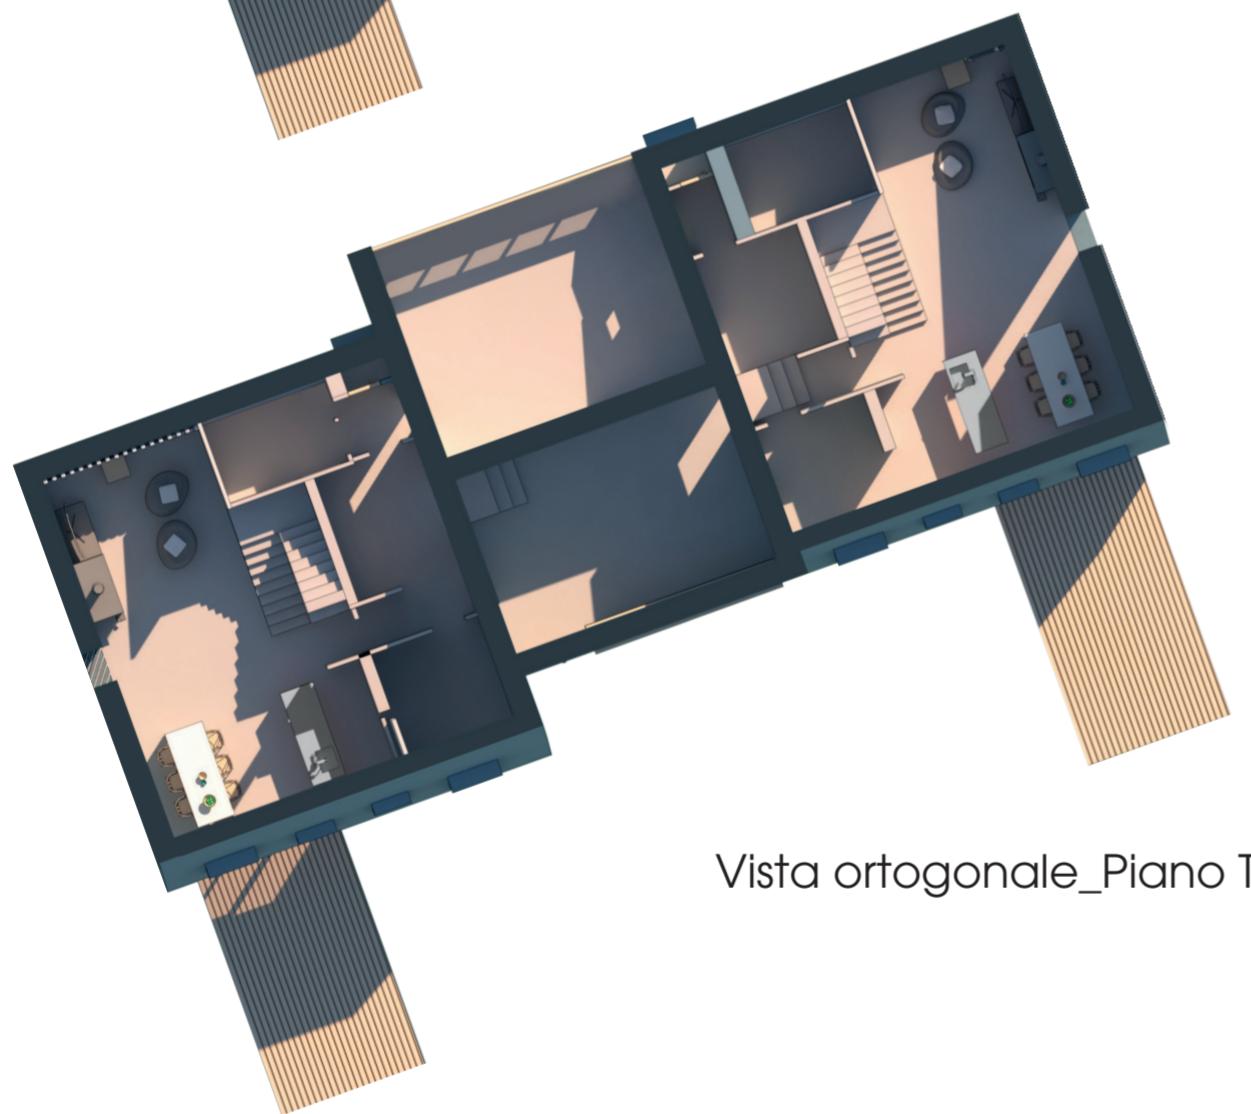

Vista ortogonale\_Piano Terra


Politecnico di Milano - Design di Interni  
A.A. 2017/2018  
Laboratorio di Modellazione Digitale  
dello Spazio  
Prof. Marco Ferrara

Studenti:


Cerini Andrea\_873112

Giussani Luca\_867909

Pucciani Francesco\_872839

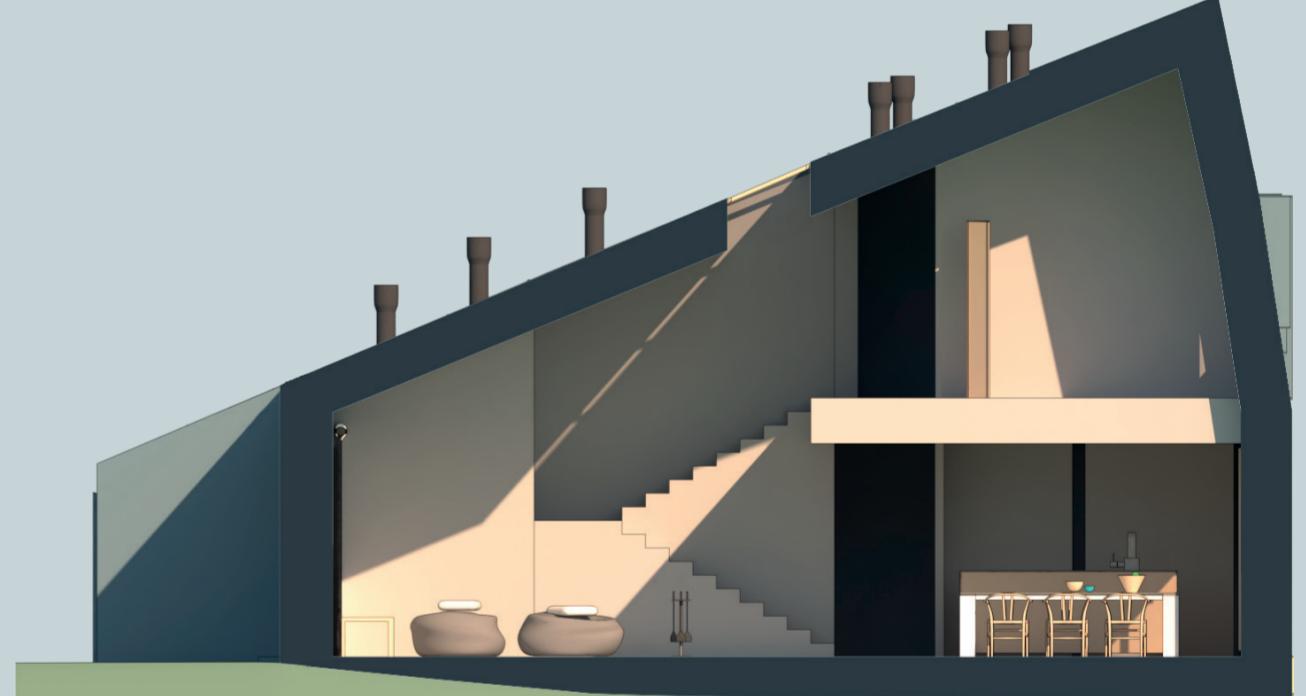


Sezione

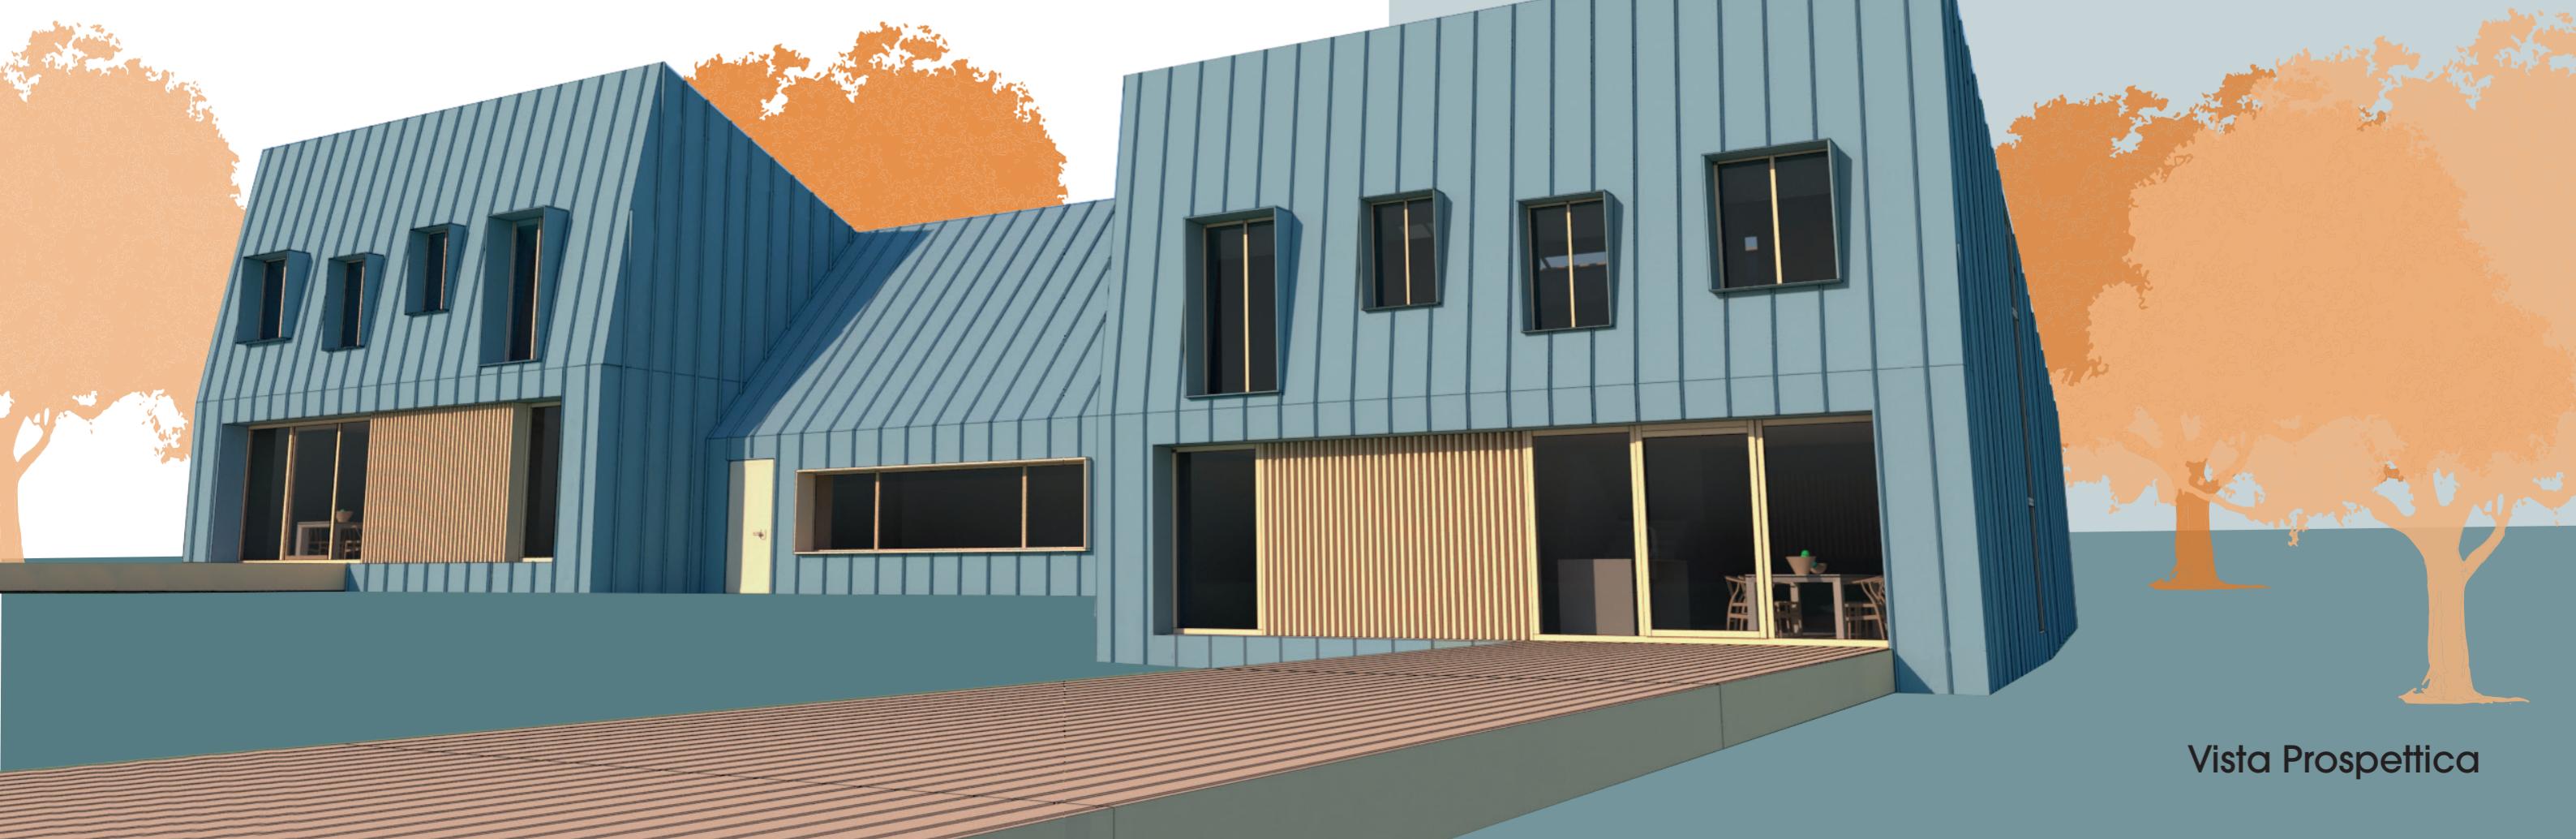

Vista Prospettica




Prospetto Anteriore

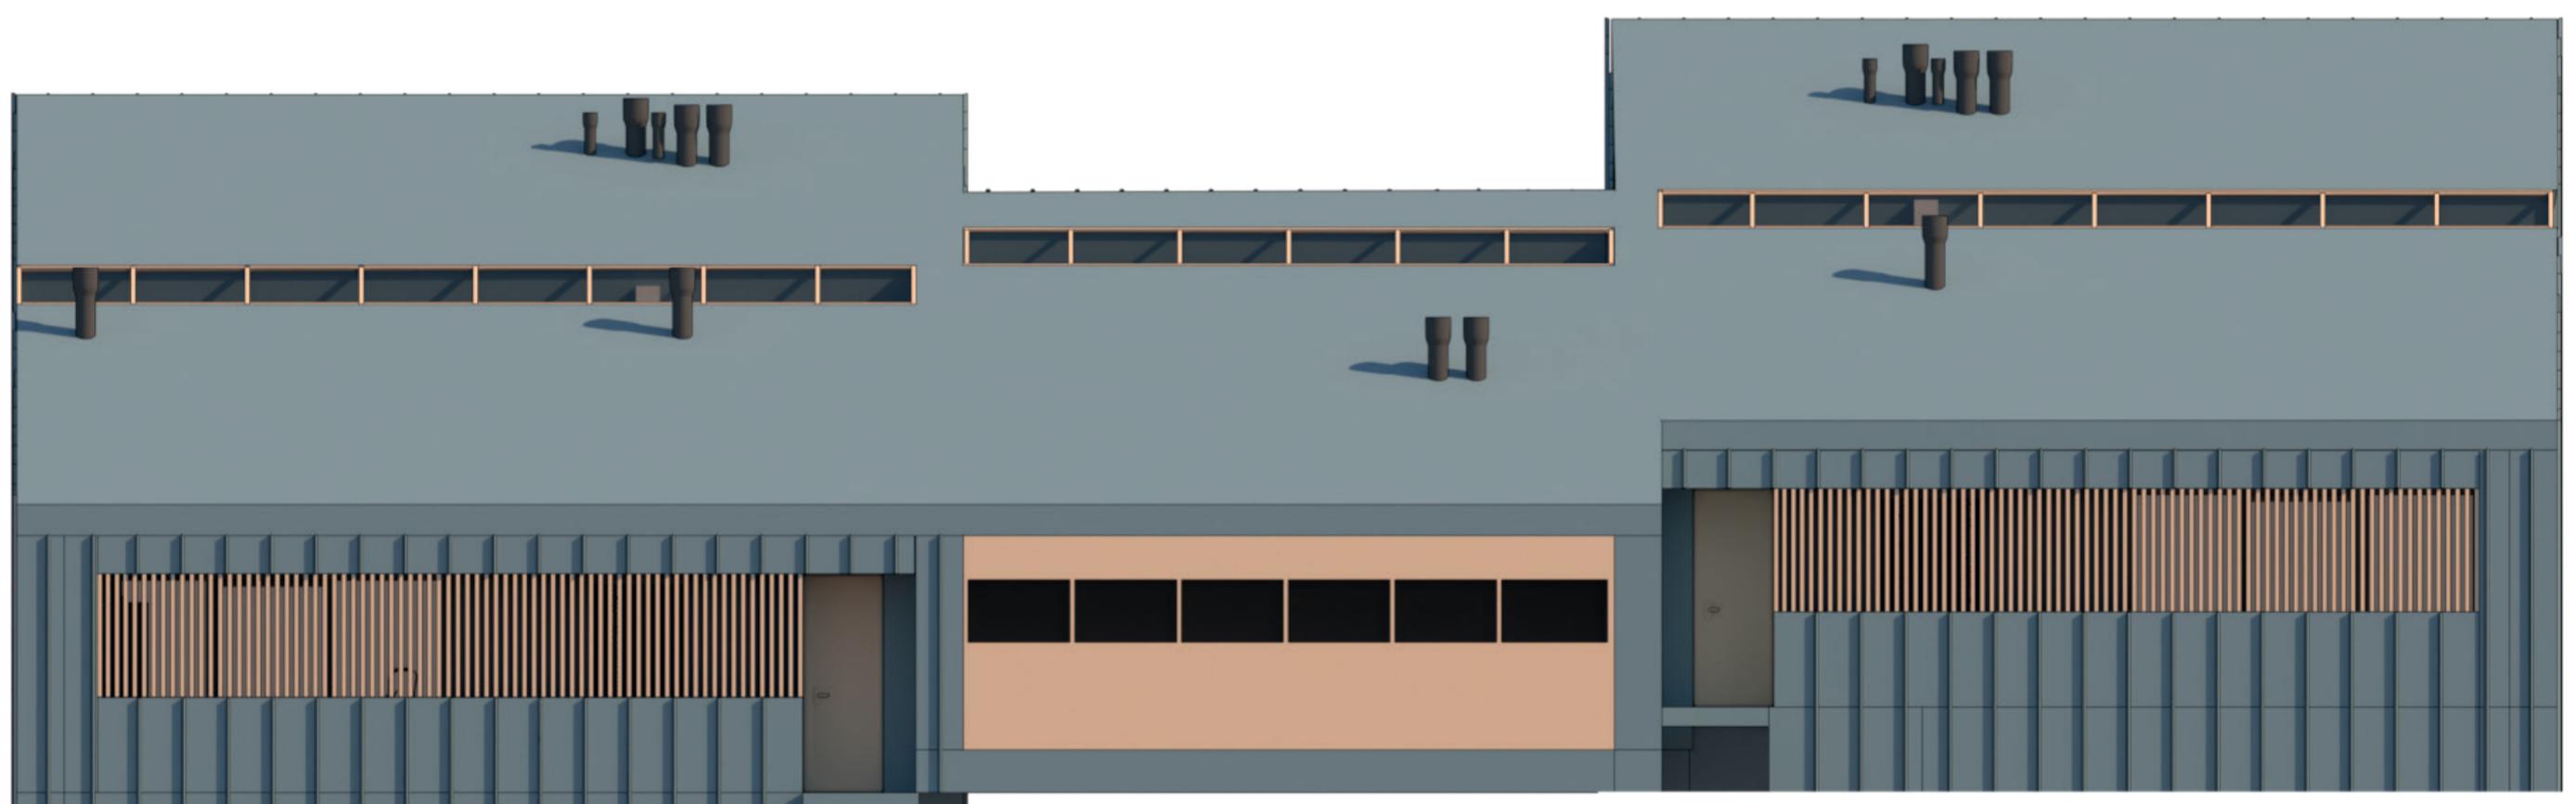


Prospetto Posteriore



Vista Prospettica

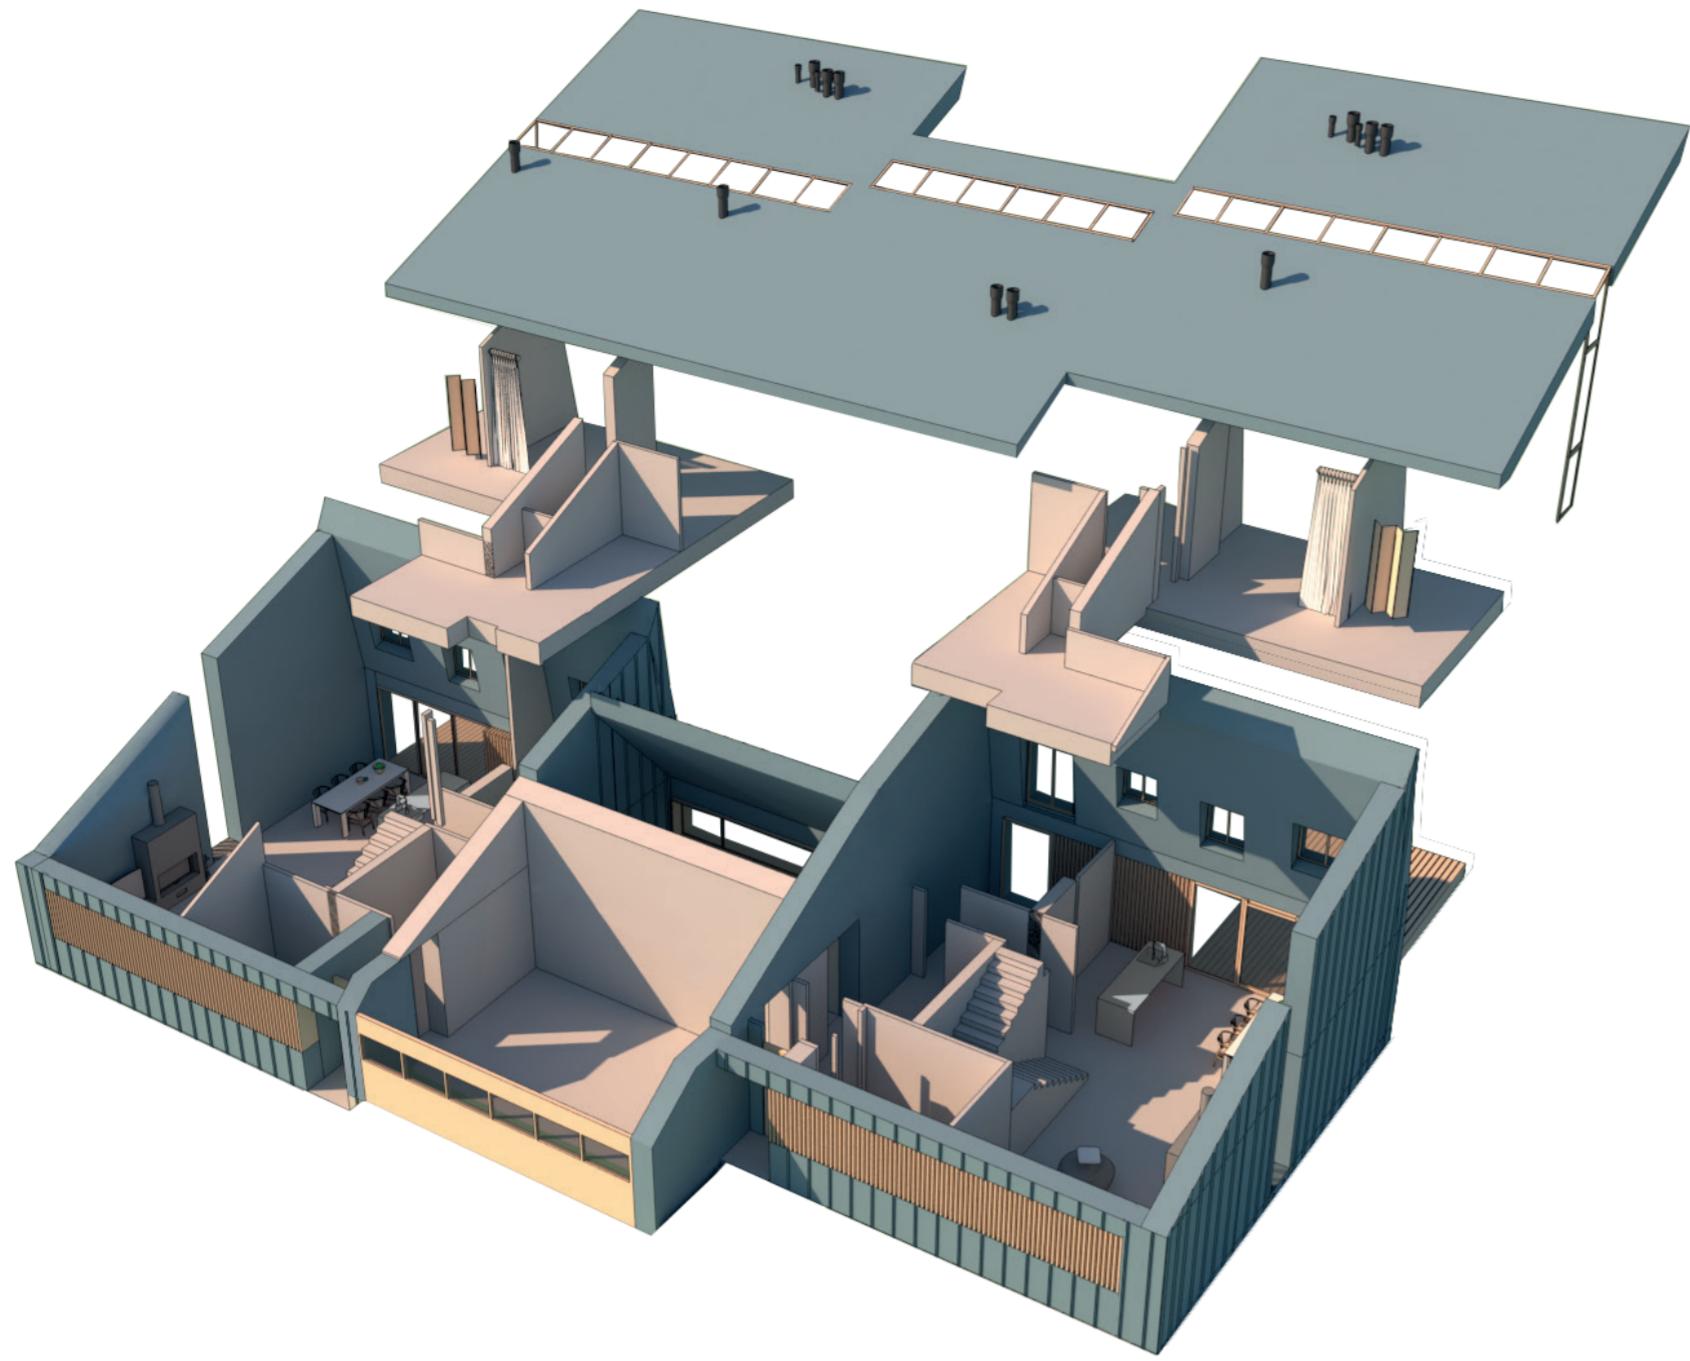

Esploso Prospettico

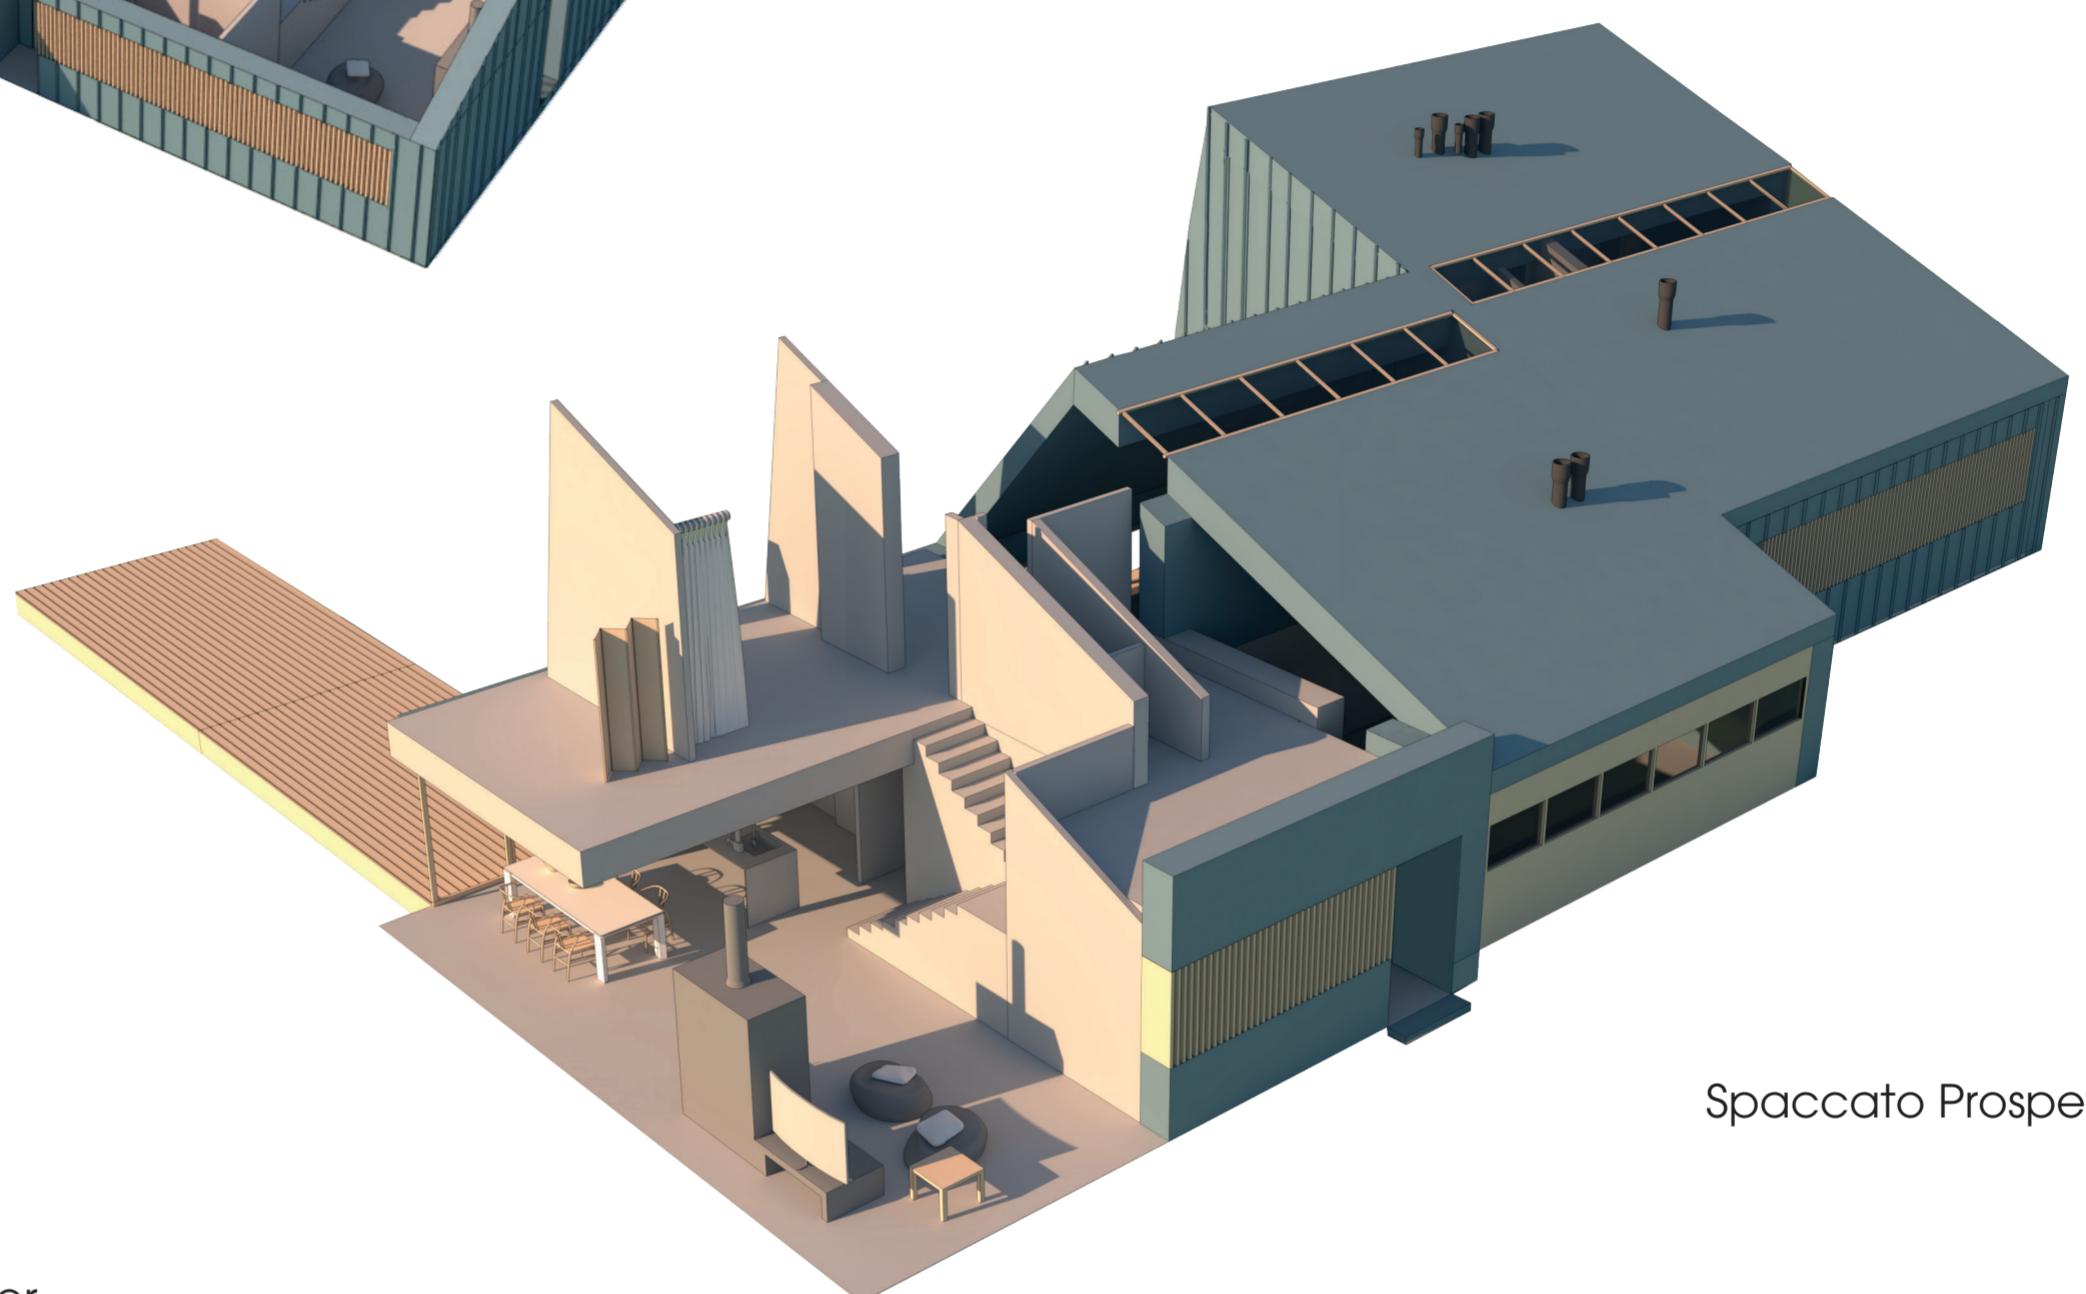

Spaccato Prospettico

Visualizzazione degli interni\_Render



**POLITECNICO**  
MILANO 1863